


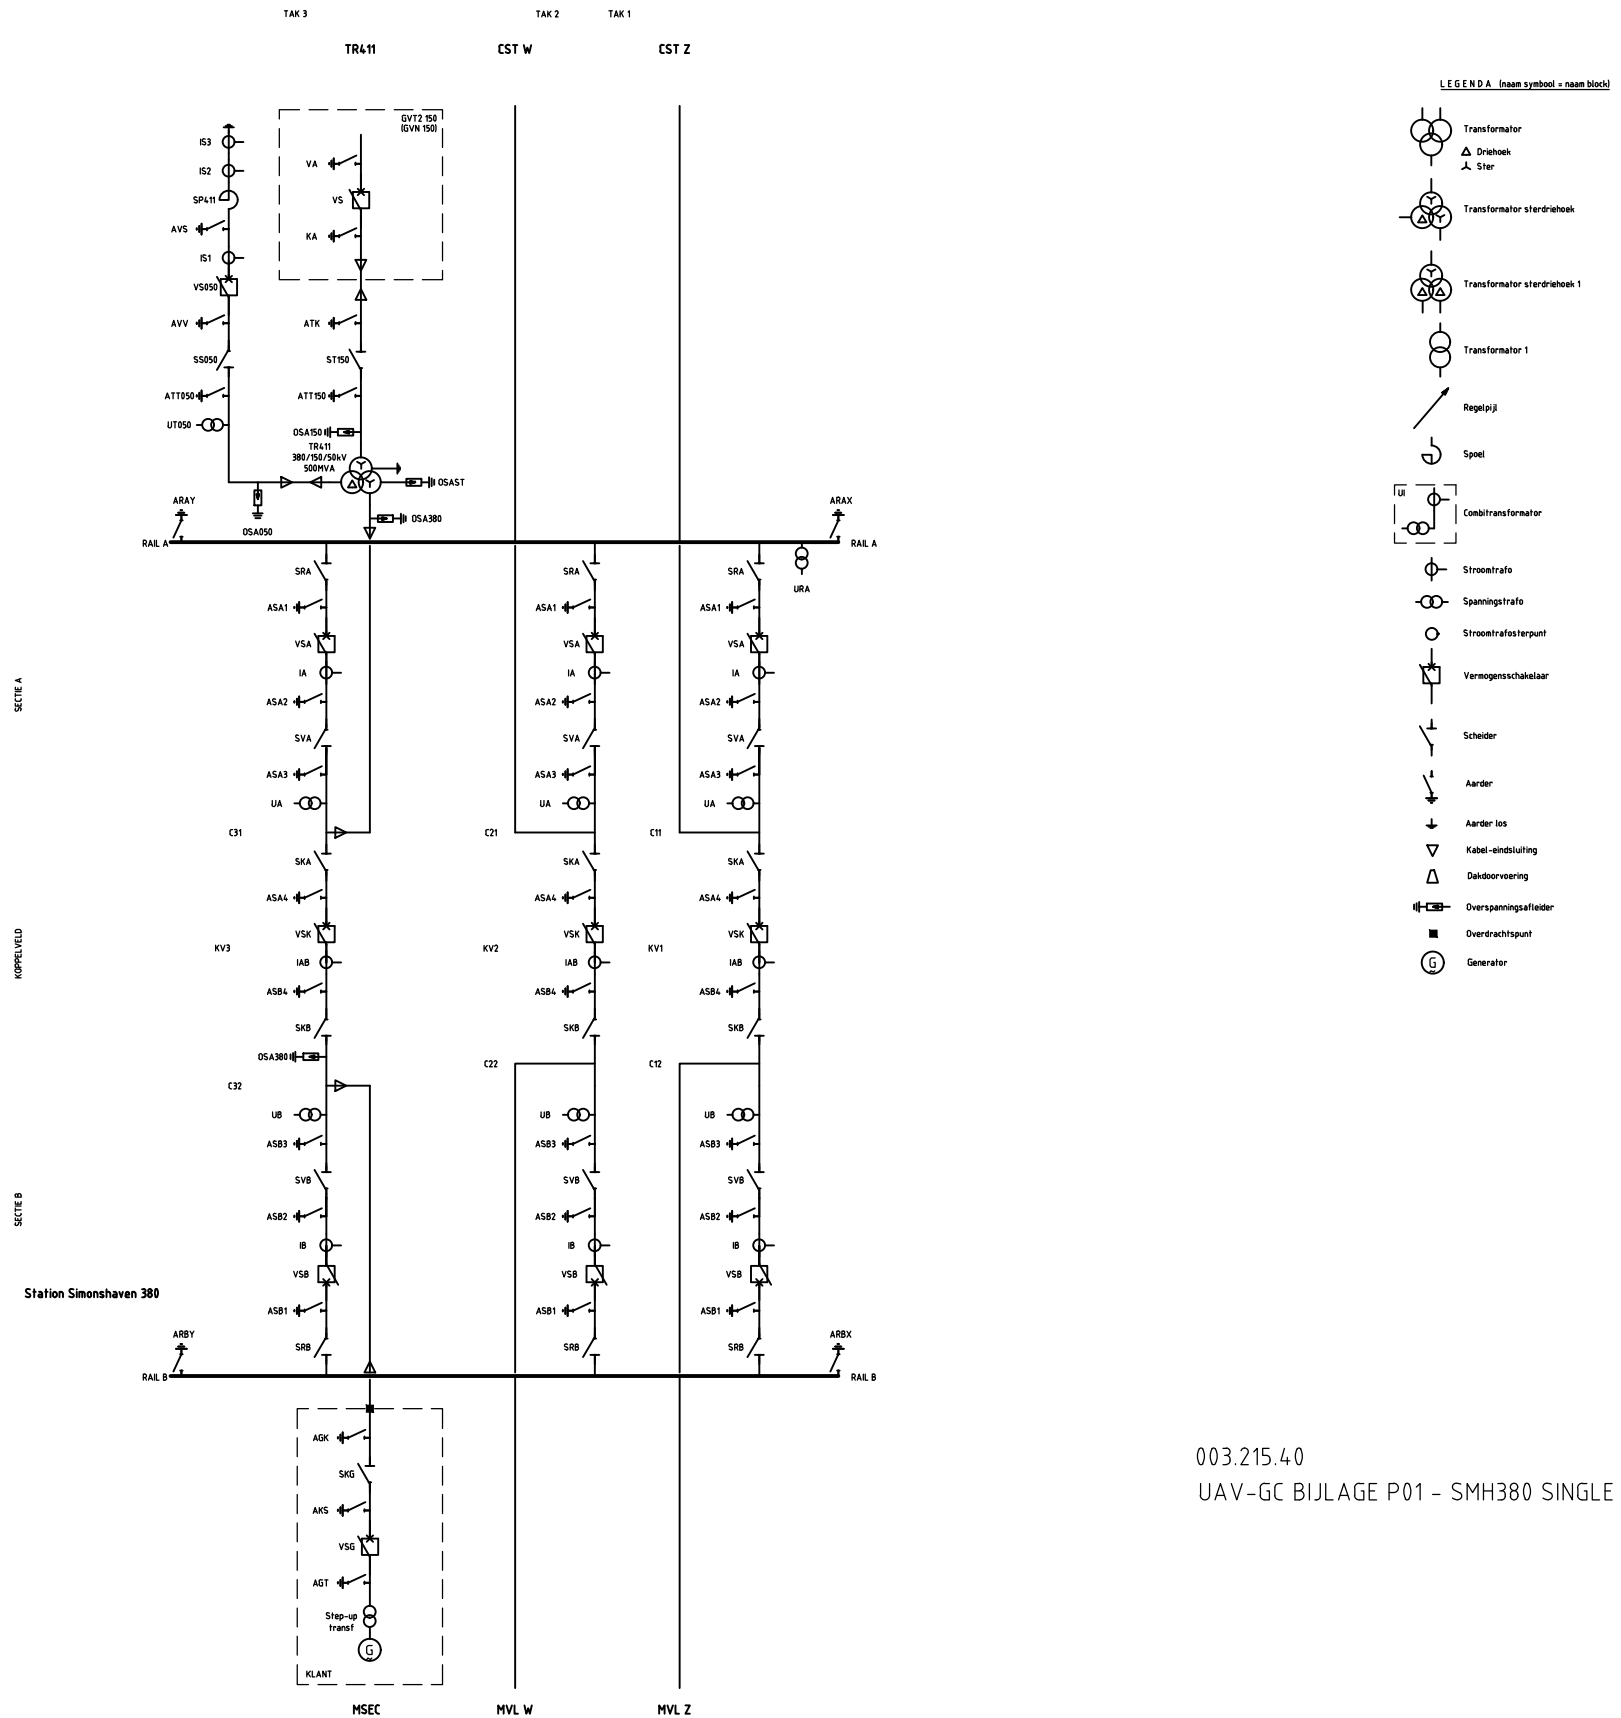

003.215.40
UAV-GC BIJLAGE P01 - SMH380 SINGLE LINE DIAGRAM - EXISTING SITUATION

Name Station Simonshaven 380					Drawing Status V00R VS1			
Relation	Rev.	Rev. Date	Rev. Description	Drawn By:	Date As-Built	Scale	Format	Object ID SMH380
	1.0	12-01-2024	Fixed Issues with Werkaanvraag en Normale Layers	JGN - TenneT		1:1	A3	
Old Drawing Number					Theme	Primair		Description: Eénlijnschema Fase 1 Eindsituatie
					Category	Schema		Document number:
					Documentcode	Grondschema		B0-01350-04-199