




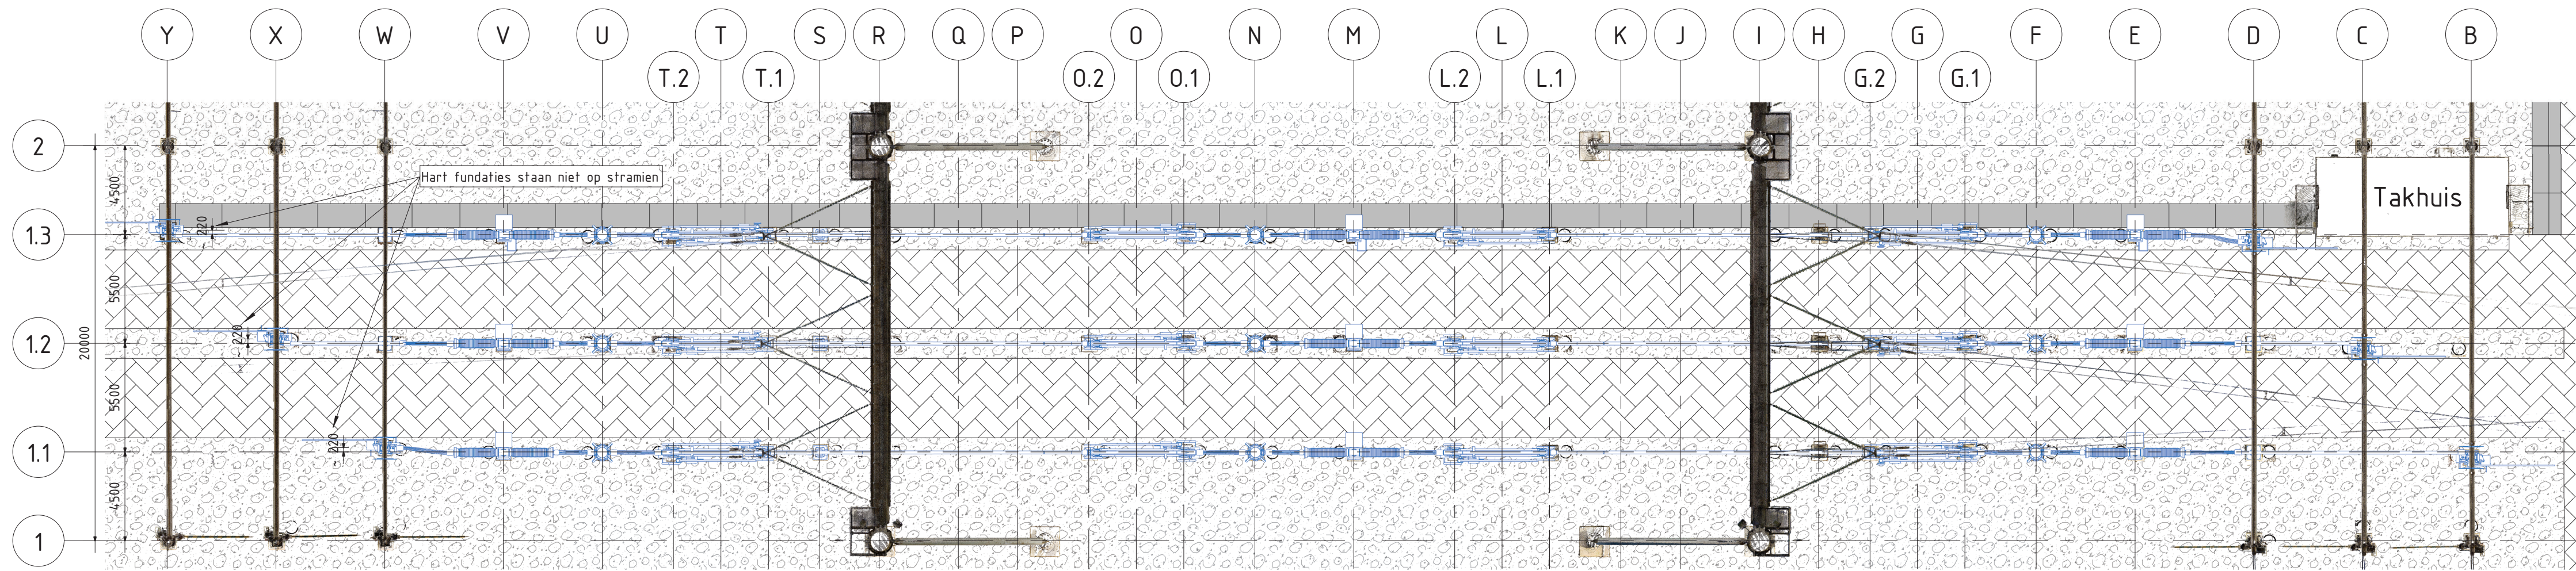

1 **Bovenaanzicht**
Schaal 1 : 200

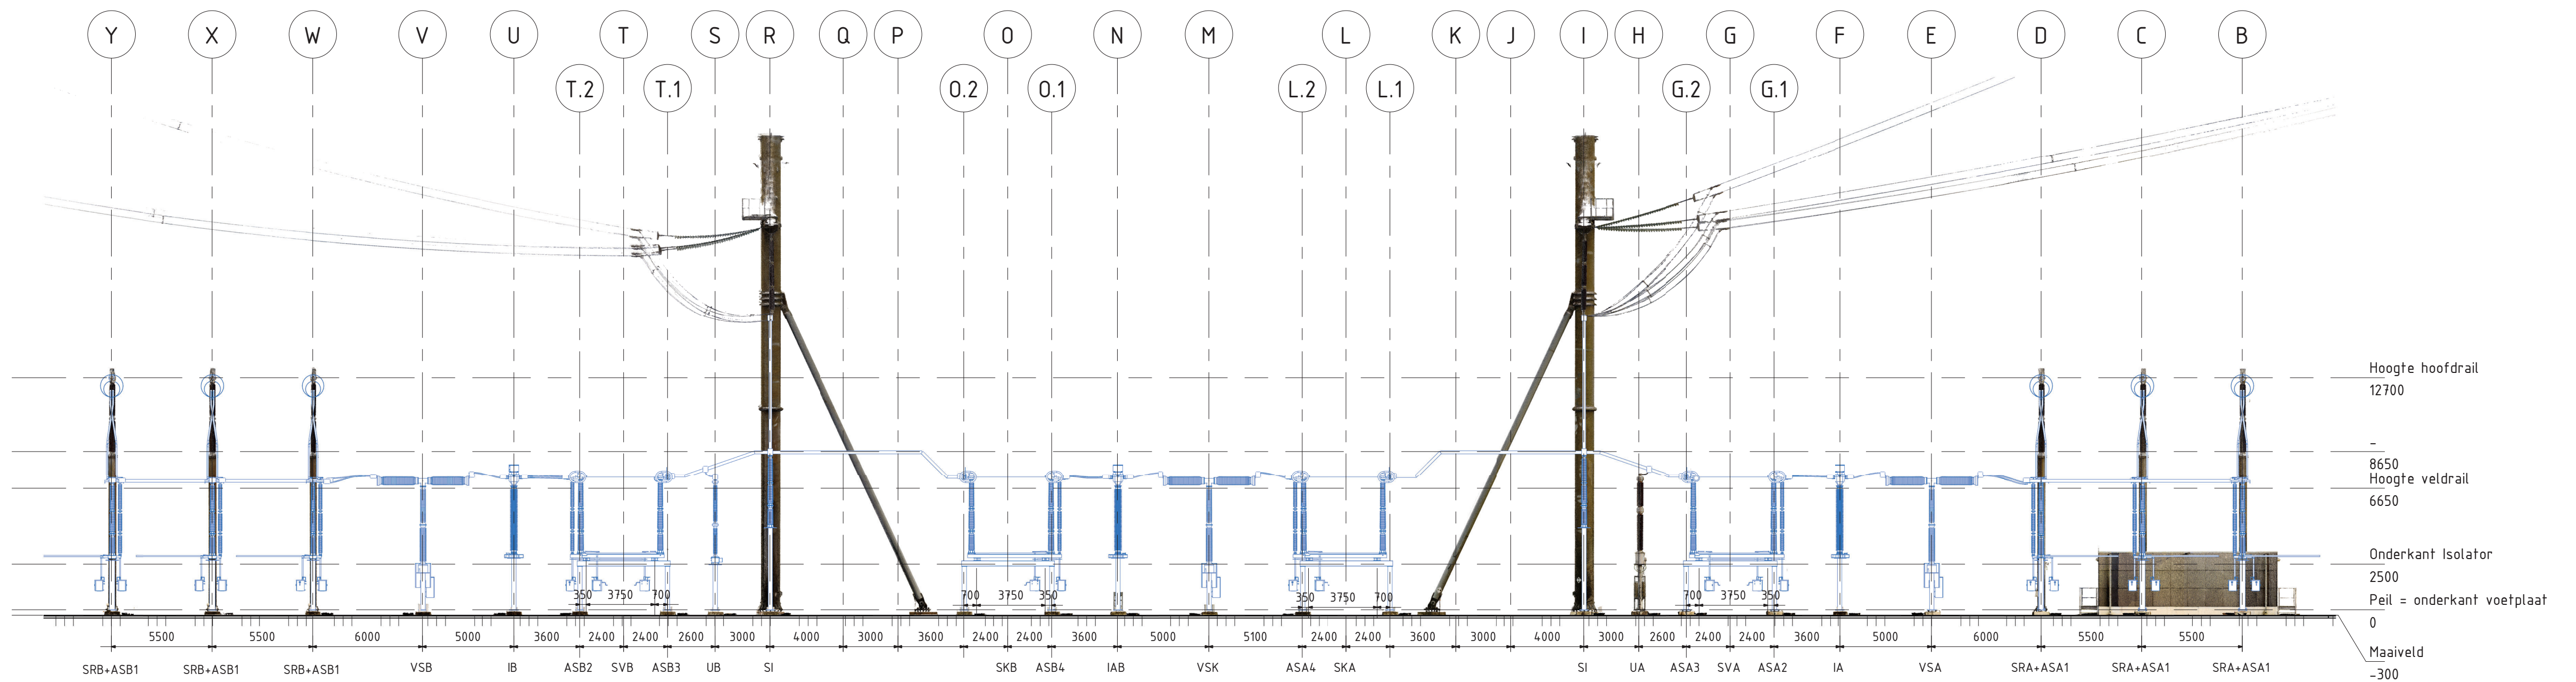

2 **Zijaanzicht**
Schaal 1 : 200

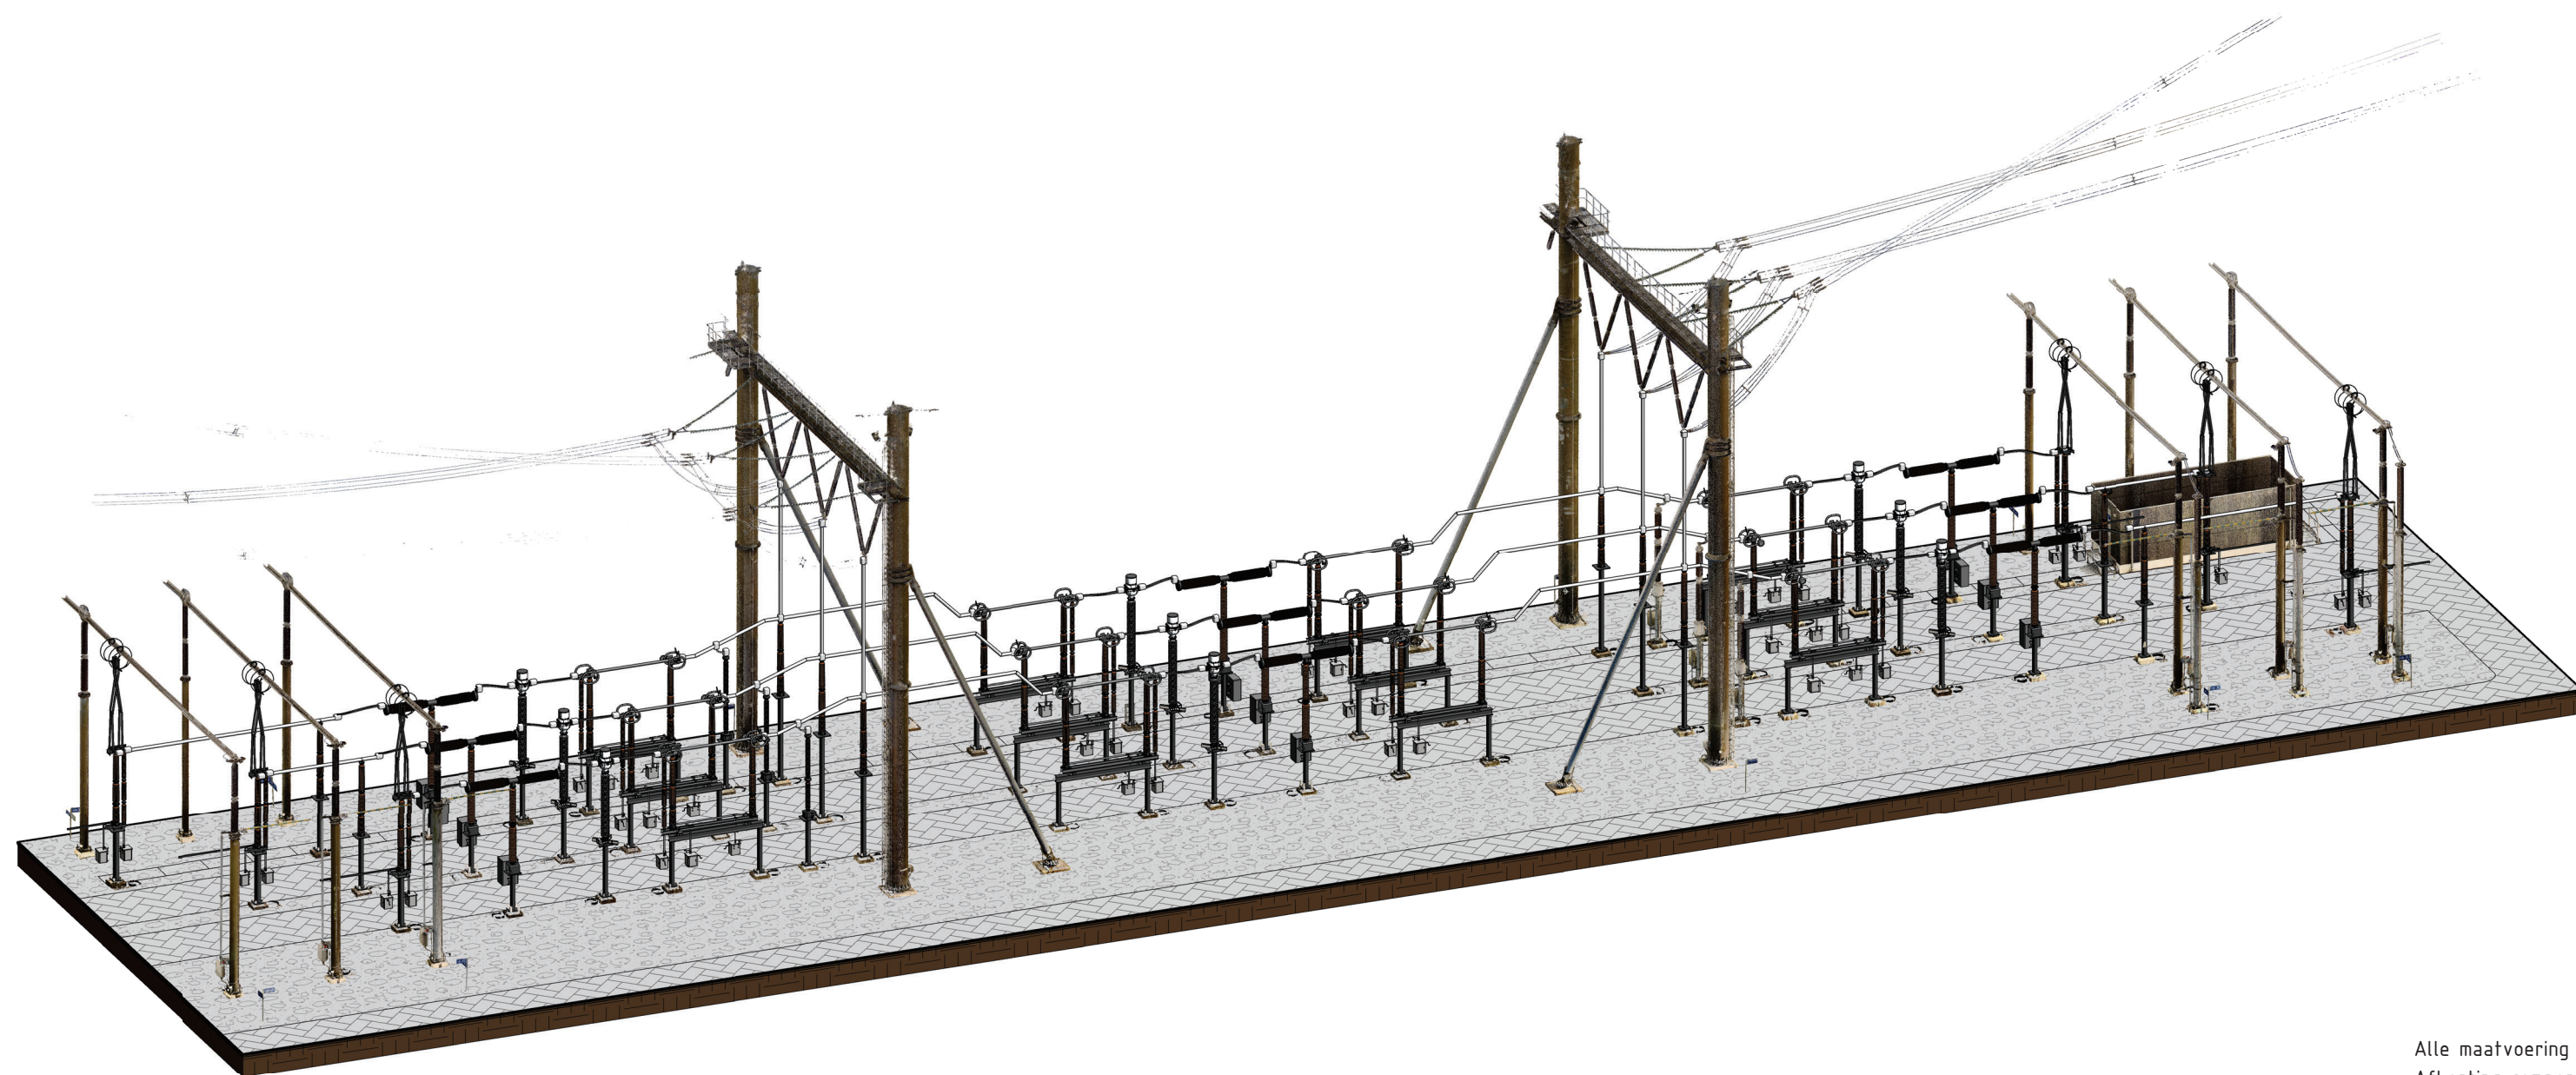

3 **3D - tak 1**
Schaal

Alle maatvoering is in mm.
Afkorting componenten o.b.v. Eenlijnschema en OGG-lijst.

Legenda	
1.	Bestaand
2.	Nieuw

Naam			Station Simonshaven 380kV		Tekeningstatus		B0	
Rev.	Datum revisie	Omschrijving revisie		Getekend	Datum As-Built	Schaal	Formaat	
C	25/08/2022	RFA Commentaar: verwerkt		Arcadis		1 : 200	A1	
Relatie				Thema	Primair (incl. EMC)			
				Categorie	Algemeen			
				Document Code	Aanzichtstekening			
				Object ID	Veld			
Oud tekeningnummer				Omschrijving	Zij- en bovenaanzicht tak 1 gewenst			
				Documentnummer	01350-01-00102			