




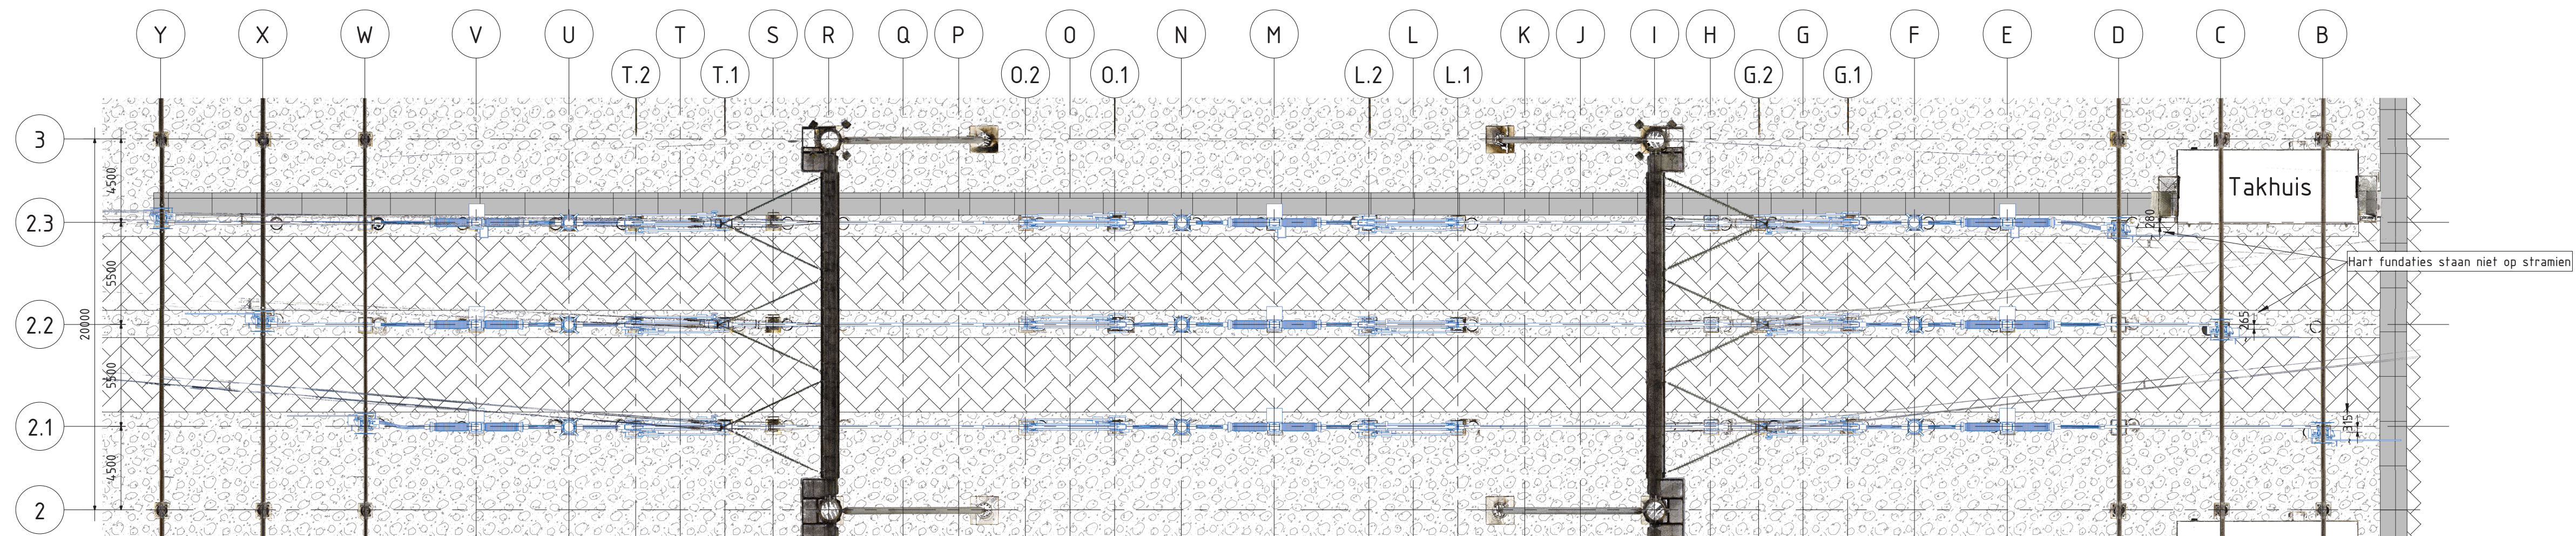

1 **Bovenaanzicht**
Schaal 1 : 200

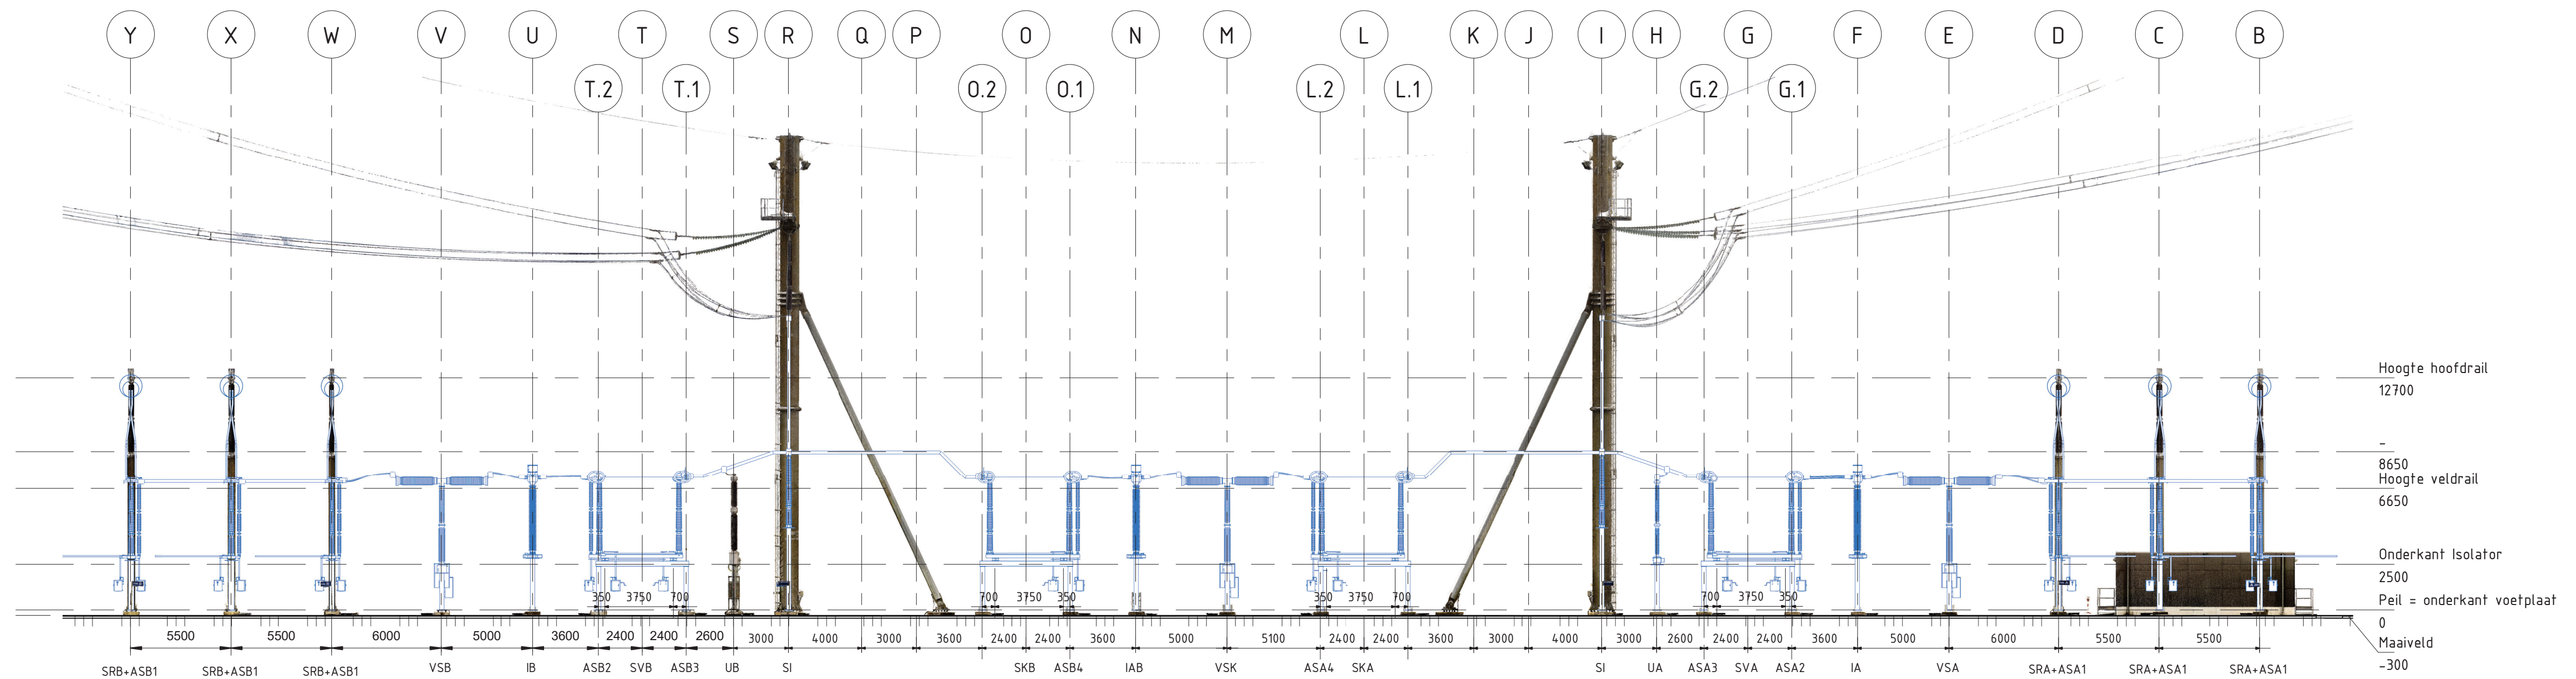

2 **Zijaanzicht**
Schaal 1 : 200

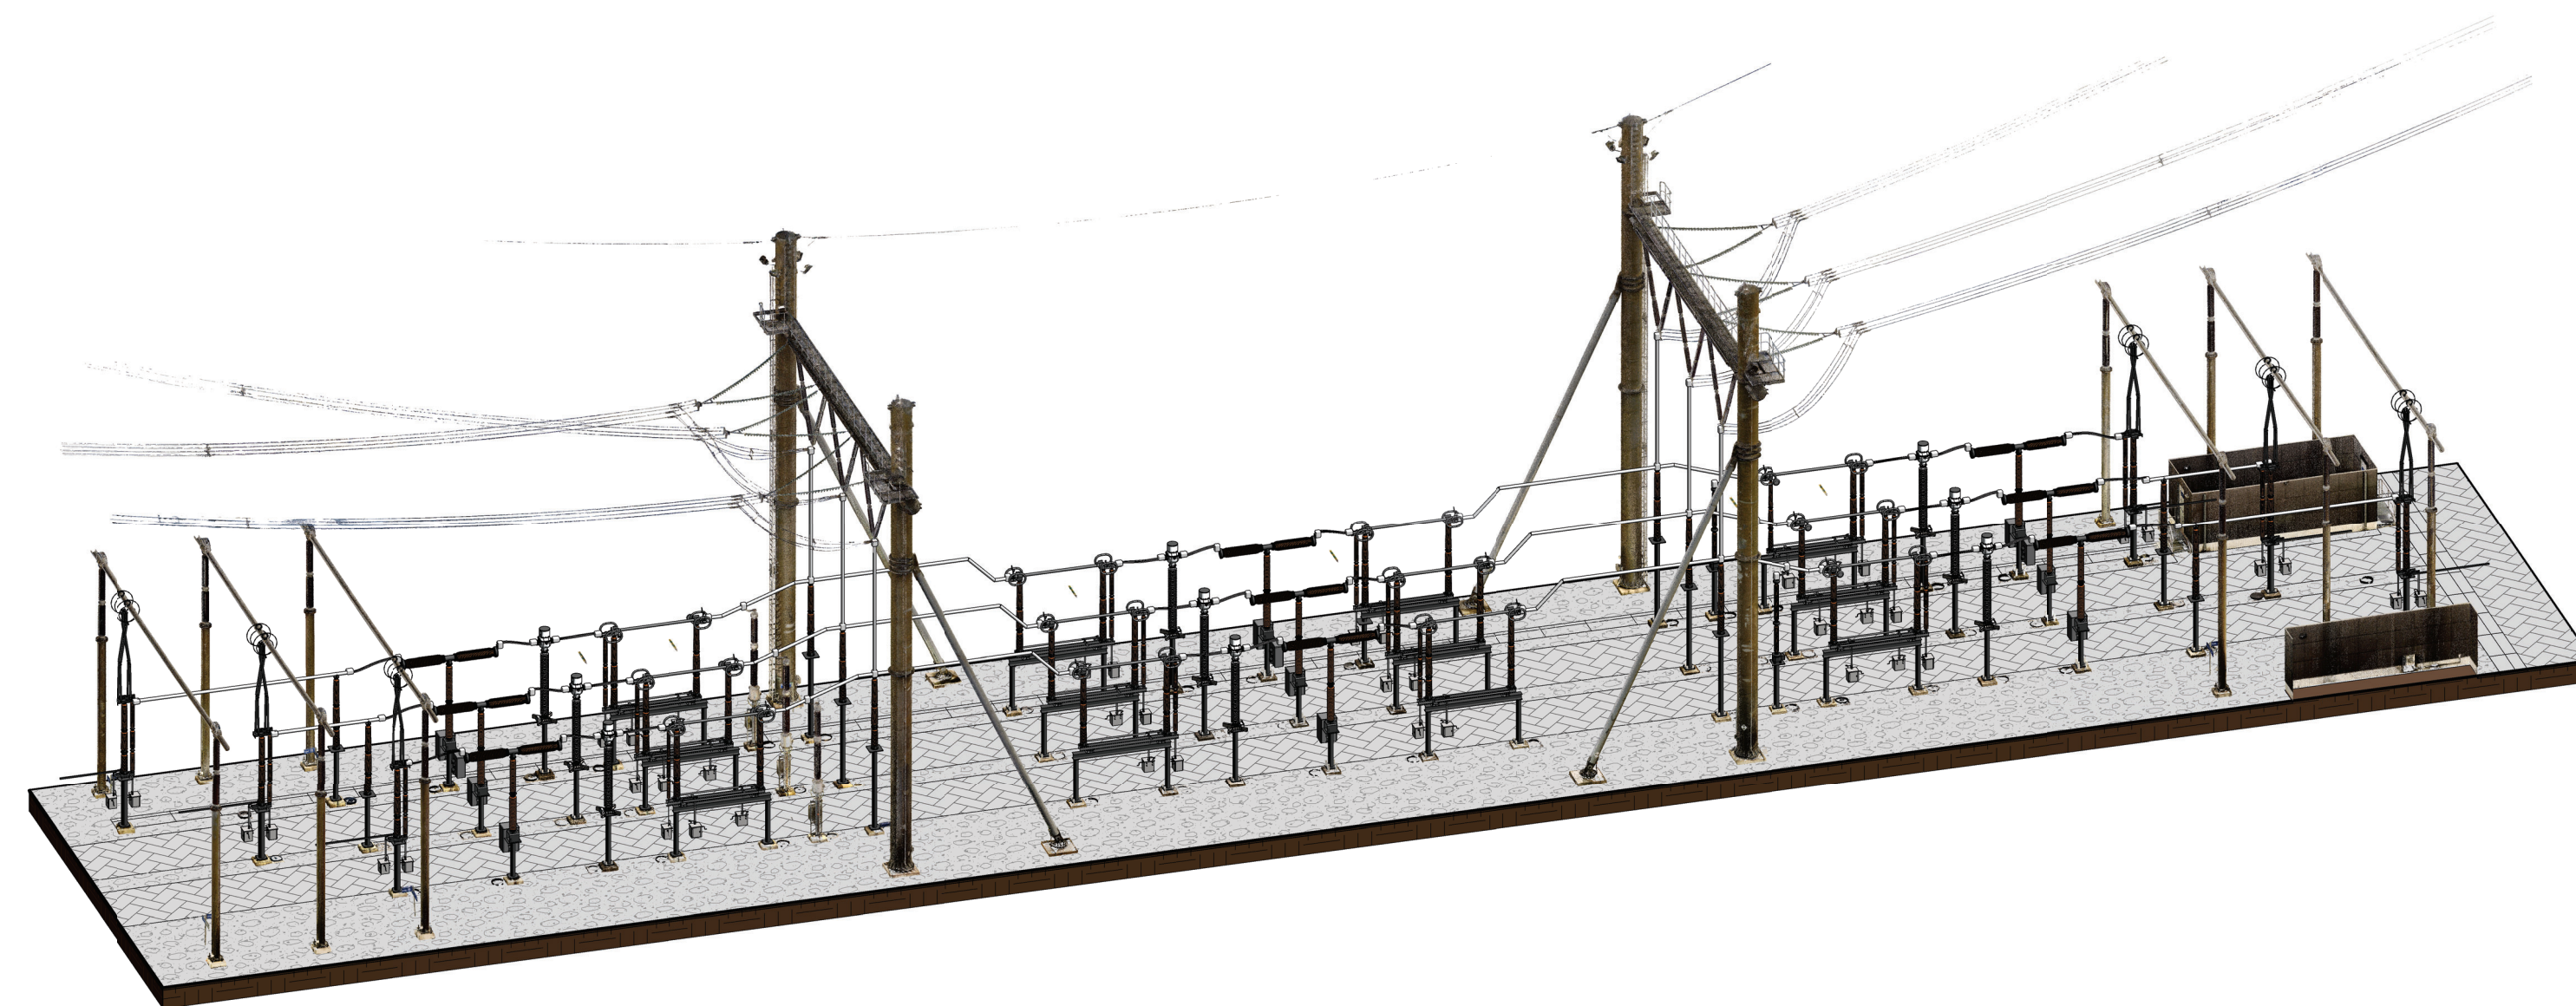

3 **3D - tak 2**
Schaal

Alle maatvoering is in mm.
Afkorting componenten o.b.v. Eenlijnschema en OGG-lijst.

Legenda

1. ☐ Bestaand
2. ☒ Nieuw

Naam			Station Simonshaven 380kV		Tekeningstatus	
					B0	
Rev.	Datum revisie	Omschrijving revisie	Getekend		Datum As-Built	Schaal
C	25/08/2022	RFA Commentaar: verwerkt	Arcadis		1 : 200	A1
Relatie			Thema	Primair (incl. EMC)		
			Categorie	Algemeen		
			Document Code	Aanzichtstekening		
			Object ID	Veld		
Oud tekeningnummer			Omschrijving	Zij- en bovenaanzicht tak 2 gewenst		
			Documentnummer	01350-01-00103		
			 Tennet Taking power further			