

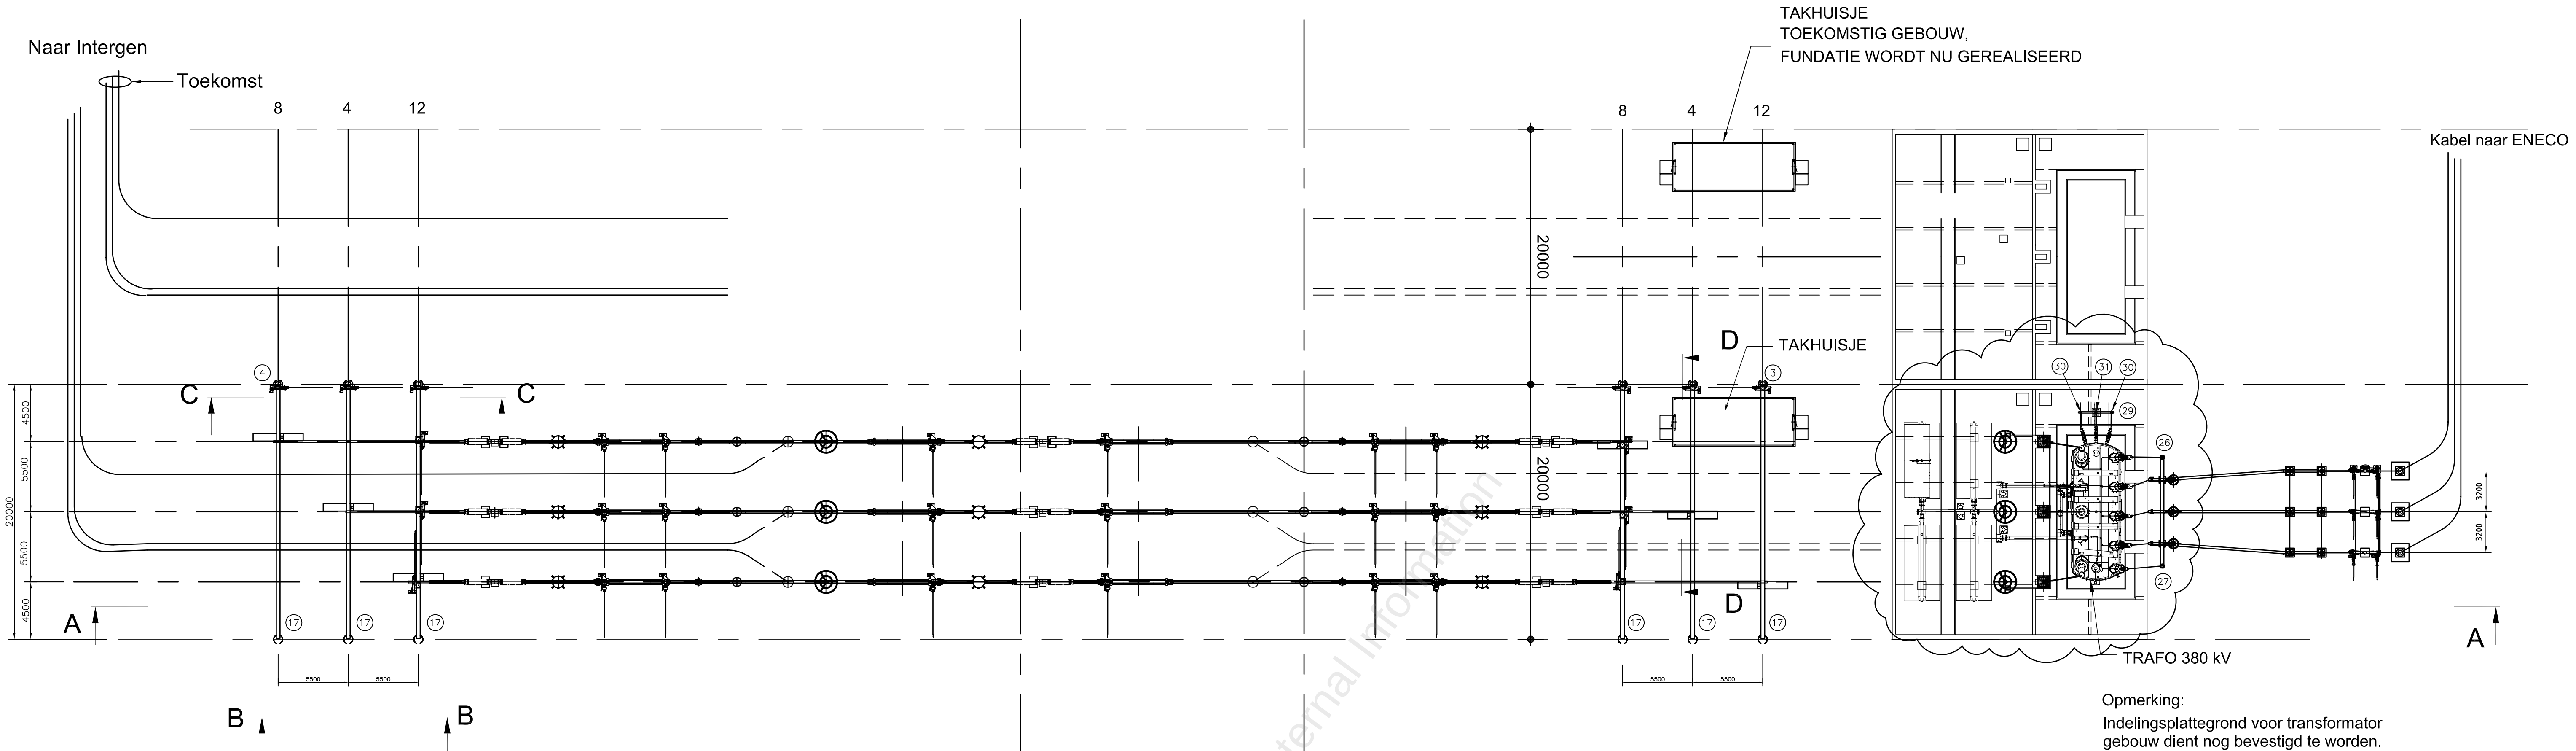
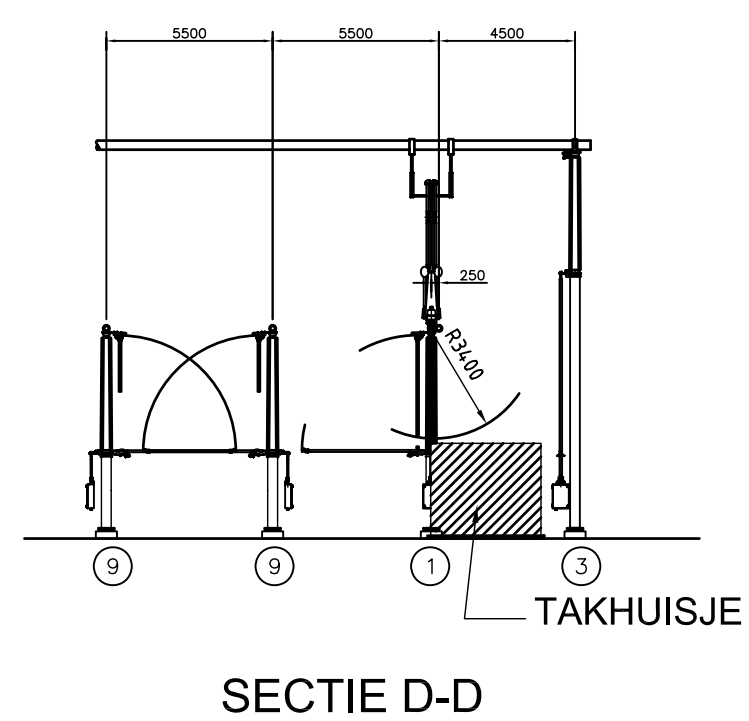
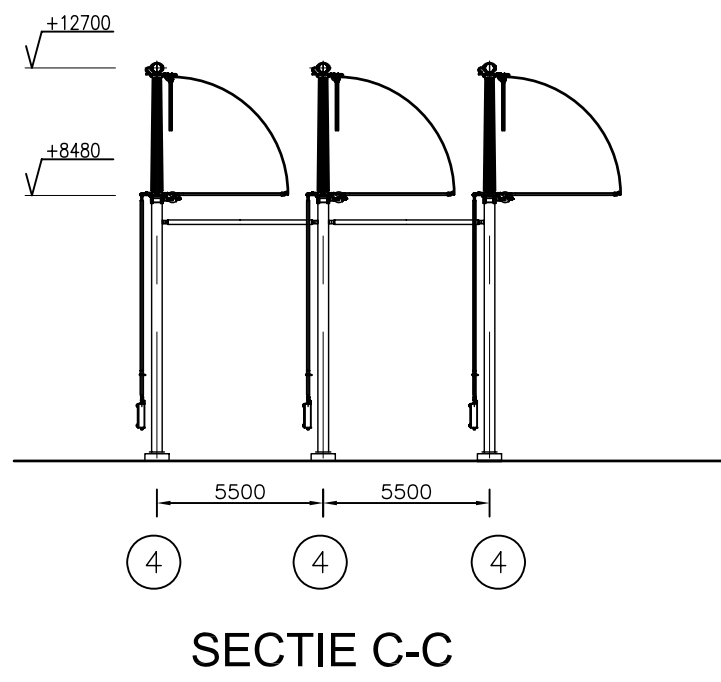


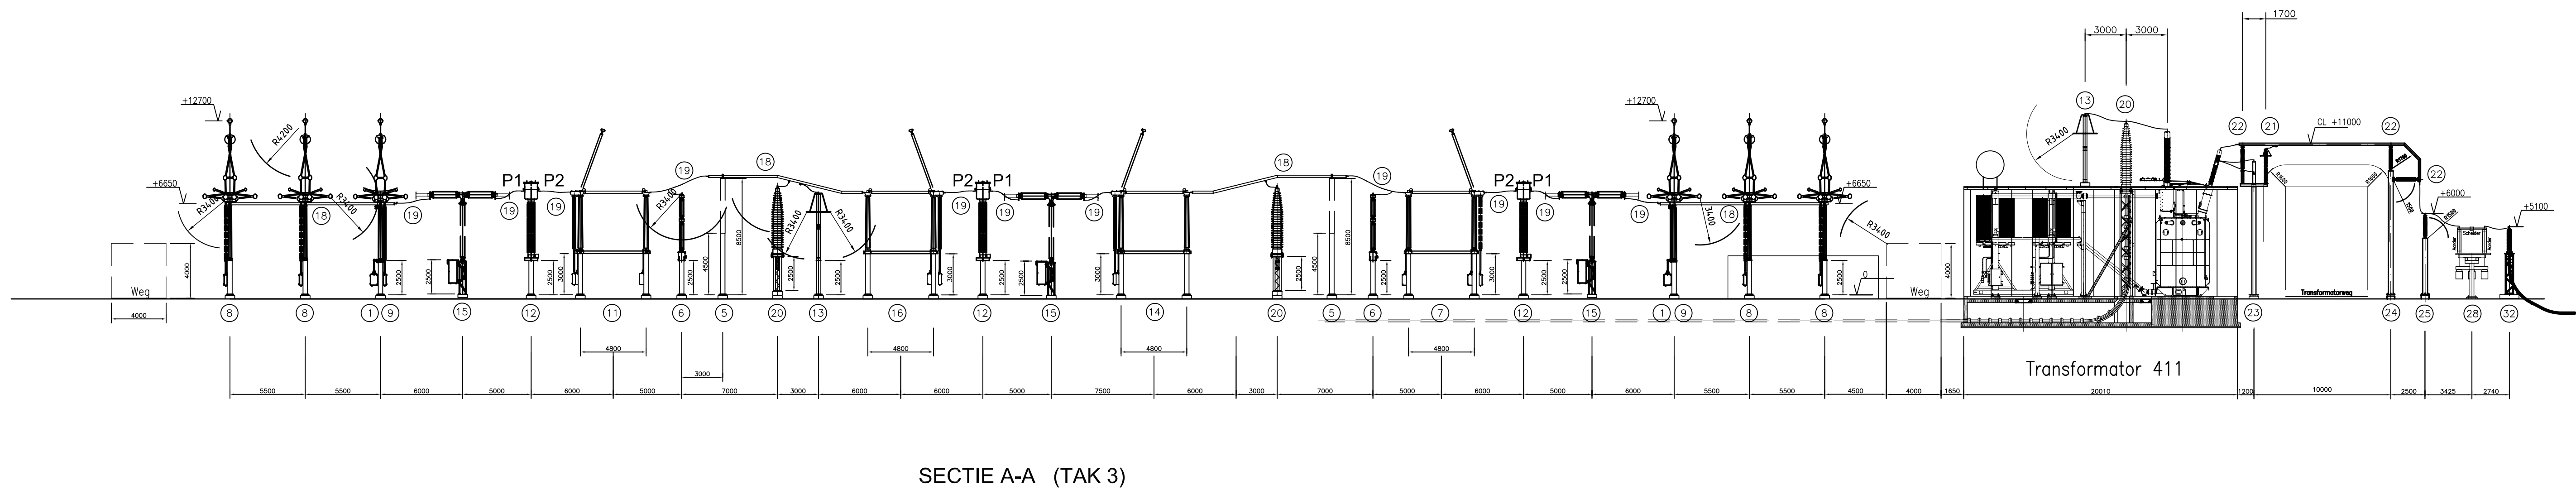

Slagwijdte Tabel		
380kV		
Fase - Aarde	3400mm	
Fase - Fase	4200mm	
150kV		
Fase - Aarde	1500mm	
Fase - Fase	1500mm	

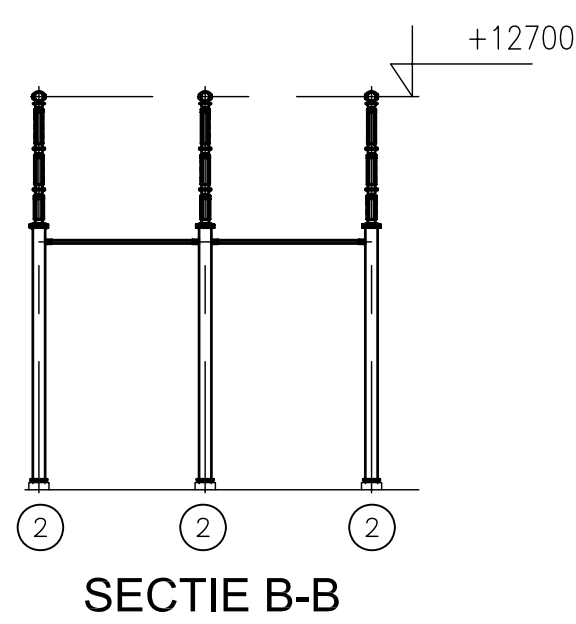

32	150kV kabelinsulatie, levering door Kabel leverancier			
31	Aardgeleider		SMH380-13-021	1
30	Overspanningsafleider	PTD H43/592856.075	SMH380-13-021	2
29	Ondersteuning		SMH380-13-021	1
28	Kolomscheider met Aangebouwde Aarder (Van beide zijden)	C403416-050	SMH380-13-010	1
27	380kV Neutral		SMH380-13-008	1
26	Overspanningsafleider Sterpunt 150kV	PTD H43/592856.055	SMH380-13-009	
25	Steunisolator	124-7270-132-101	SMH380-13-013	3
24	Ondersteuning		SMH380-13-014	1
23	Ondersteuning		SMH380-13-009	1
22	Steunisolator	124-7270-132-101	SMH380-13-014	9
21	Overspanningsafleider 150kV Fasen	PTD H43/592856.035	SMH380-13-009	1
20	380kV kabelinsulatie, levering door Kabel leverancier			
19	Flexibele aansluitingen: geleider bundel Al/Aw Ø 432 mm, type 1055/45			
18	Lijnedelen: Ø160 x 7 mm aluminium legering E-AlMg-Si 0.5 F22 volgens DIN 1725 en DIN 45001			
17	Hoofd rail systeem: Ø300 x 8 mm aluminium legering E-AlMg-Si 0.5 F22 volgens DIN 1725 en DIN 45001			
16	Klopscheider met Rën aangebouwde aarder "links"	C403416-030	SMH380-13-018	3
15	Vermogensschakelaar	1H5B100001M983		9
14	Klopscheider met Rën aangebouwde aarder "rechts"	C403416-31	SMH380-13-019	3
13	Overspanningsafleider 380kV Fasen	PTD H43/592856.025	SMH380-13-008	9
12	Stroomtransformator	212743	SMH380-13-007	9
11	Klopscheider met twee aangebouwde aarders "rechts"	C403416-041	SMH380-13-017	3
10	Niet Gebruikt			
9	Klopaarder "rechts" (takrail)	C403416-020	SMH380-13-002	4
8	Pantografscheider zonder aarder	C403416-015	SMH380-13-001	4
7	Klopscheider met twee aangebouwde aarders "links"	C403416-040	SMH380-13-005	3
6	Spanningstransformator	H3-7375 Rev C	SMH380-13-006	6
5	Steunisolator		SMH380-13-011	6
4	Klopaarder hoofd rail "links"	C403416-020	SMH380-13-003	3
3	Klopaarder hoofd rail "rechts"	C403416-021	SMH380-13-016	3
2	Steunisolator		SMH380-13-020	6
1	Pantograaf scheider met aarders "rechts"	C403416-010	SMH380-13-015	2
No.	Omschrijving	Tekening Nummer	Ondersteuning Tekening Nummer	Qty

C

B

A

Slagwijdten aangegeven, diverse kleine aanpassingen

28/7/06

ETW

Na wijziging

Datum

Naam

Opgstellingsplattegrond en Zij aanzicht

Tak 3

380kV Station Simonshaven

Schaal: 1:250

Formaat: TF A0

Naam: E.T. Wren

Datum: 12/7/07

Tennet

Utrechtseweg 310

6515 AS ARNHEM

Tel: 026-373111

Fax: 026-373112

Postbus 718

6800 AS ARNHEM

E-mail: Servicecentrum@tennet.nl

Internet: www.tennet.nl

Identificatienummer: SMH380-11-005-001

AutoCAD tekening: SMH380-11-005-001.DWG

Postbus 2855

3500 GW Utrecht

Tel: 030 - 265 5555

CT TFC