


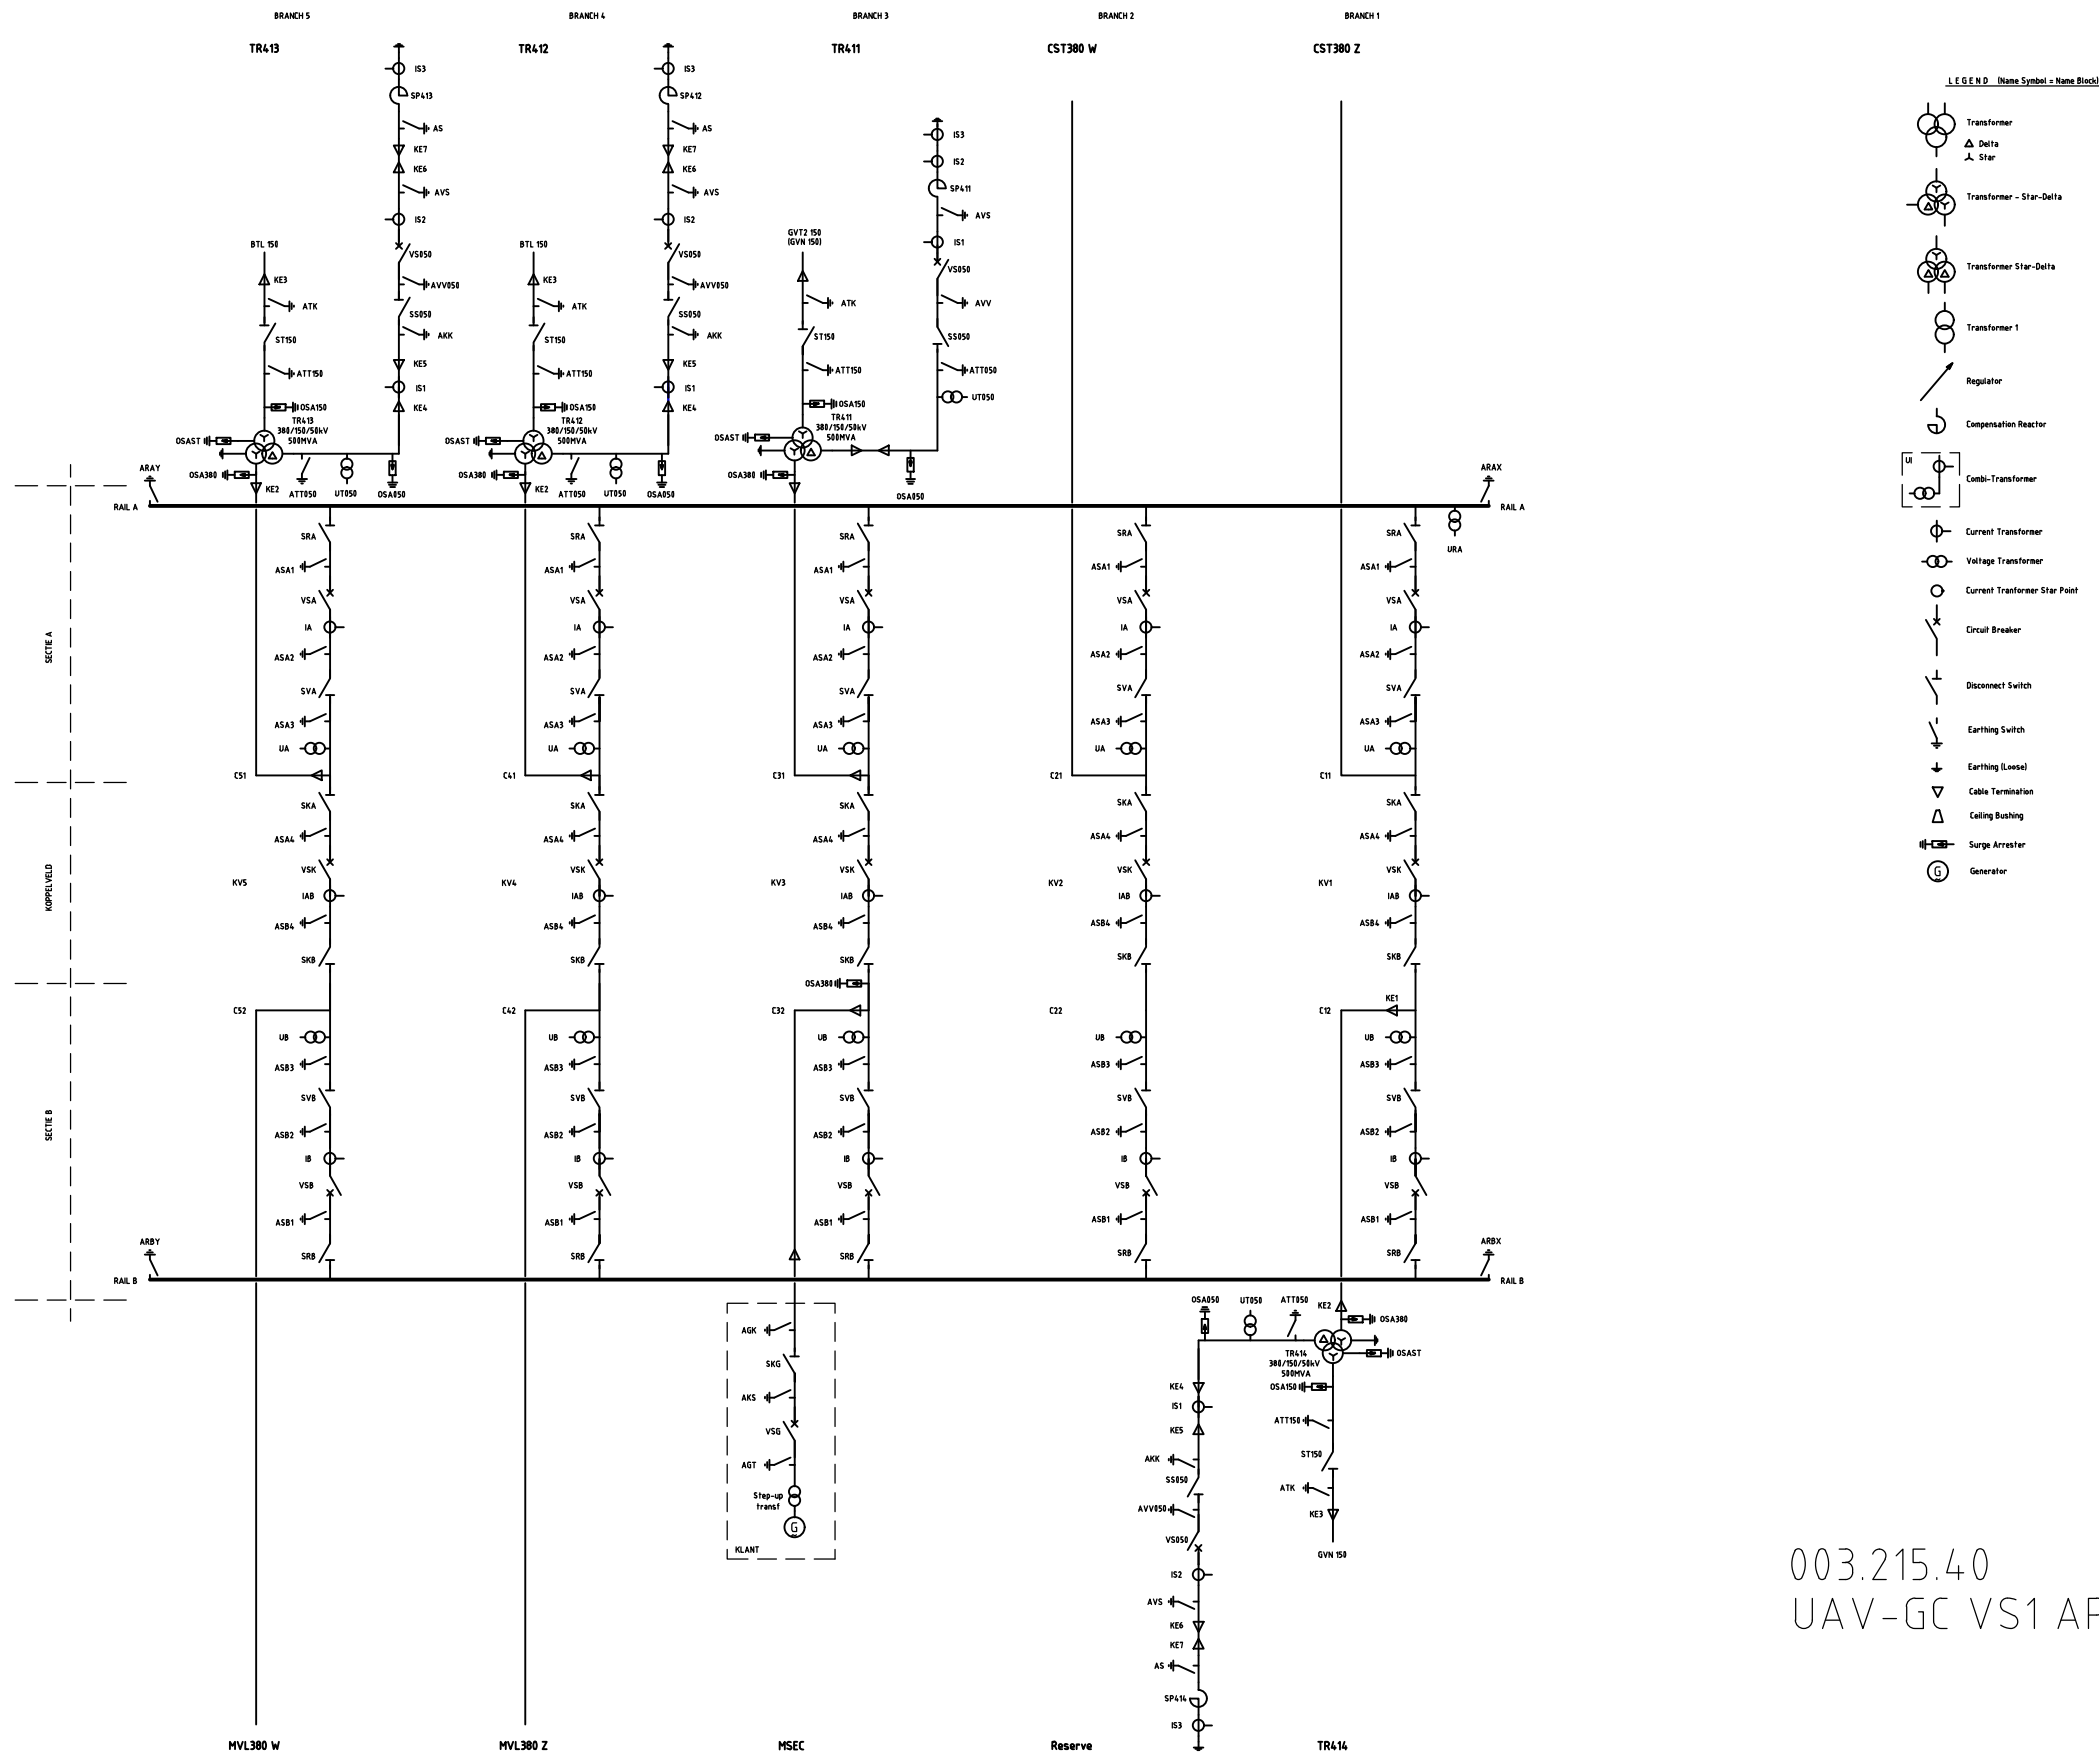

003.215.40
UAV-GC VS1 APPENDIX P14

Name Station Simonshaven 380					Drawing Status V00R VS1				
Relation	Rev.	Rev. Date	Rev. Description	Drawn By:	Date As-Built	Scale	Format	Object ID	
	1.0	17-01-2024		JGN - TenneT		1:1	A3	SMH380	
					Theme	Primair		Description: SMH380 PHASE 2-4 SINGLE LINE DIAGRAM STATION - DESIRED END SITUATION	
					Category	Schema			
Old Drawing Number					Documentcode	Grondschema		Document number: B0-01350-04-153	