
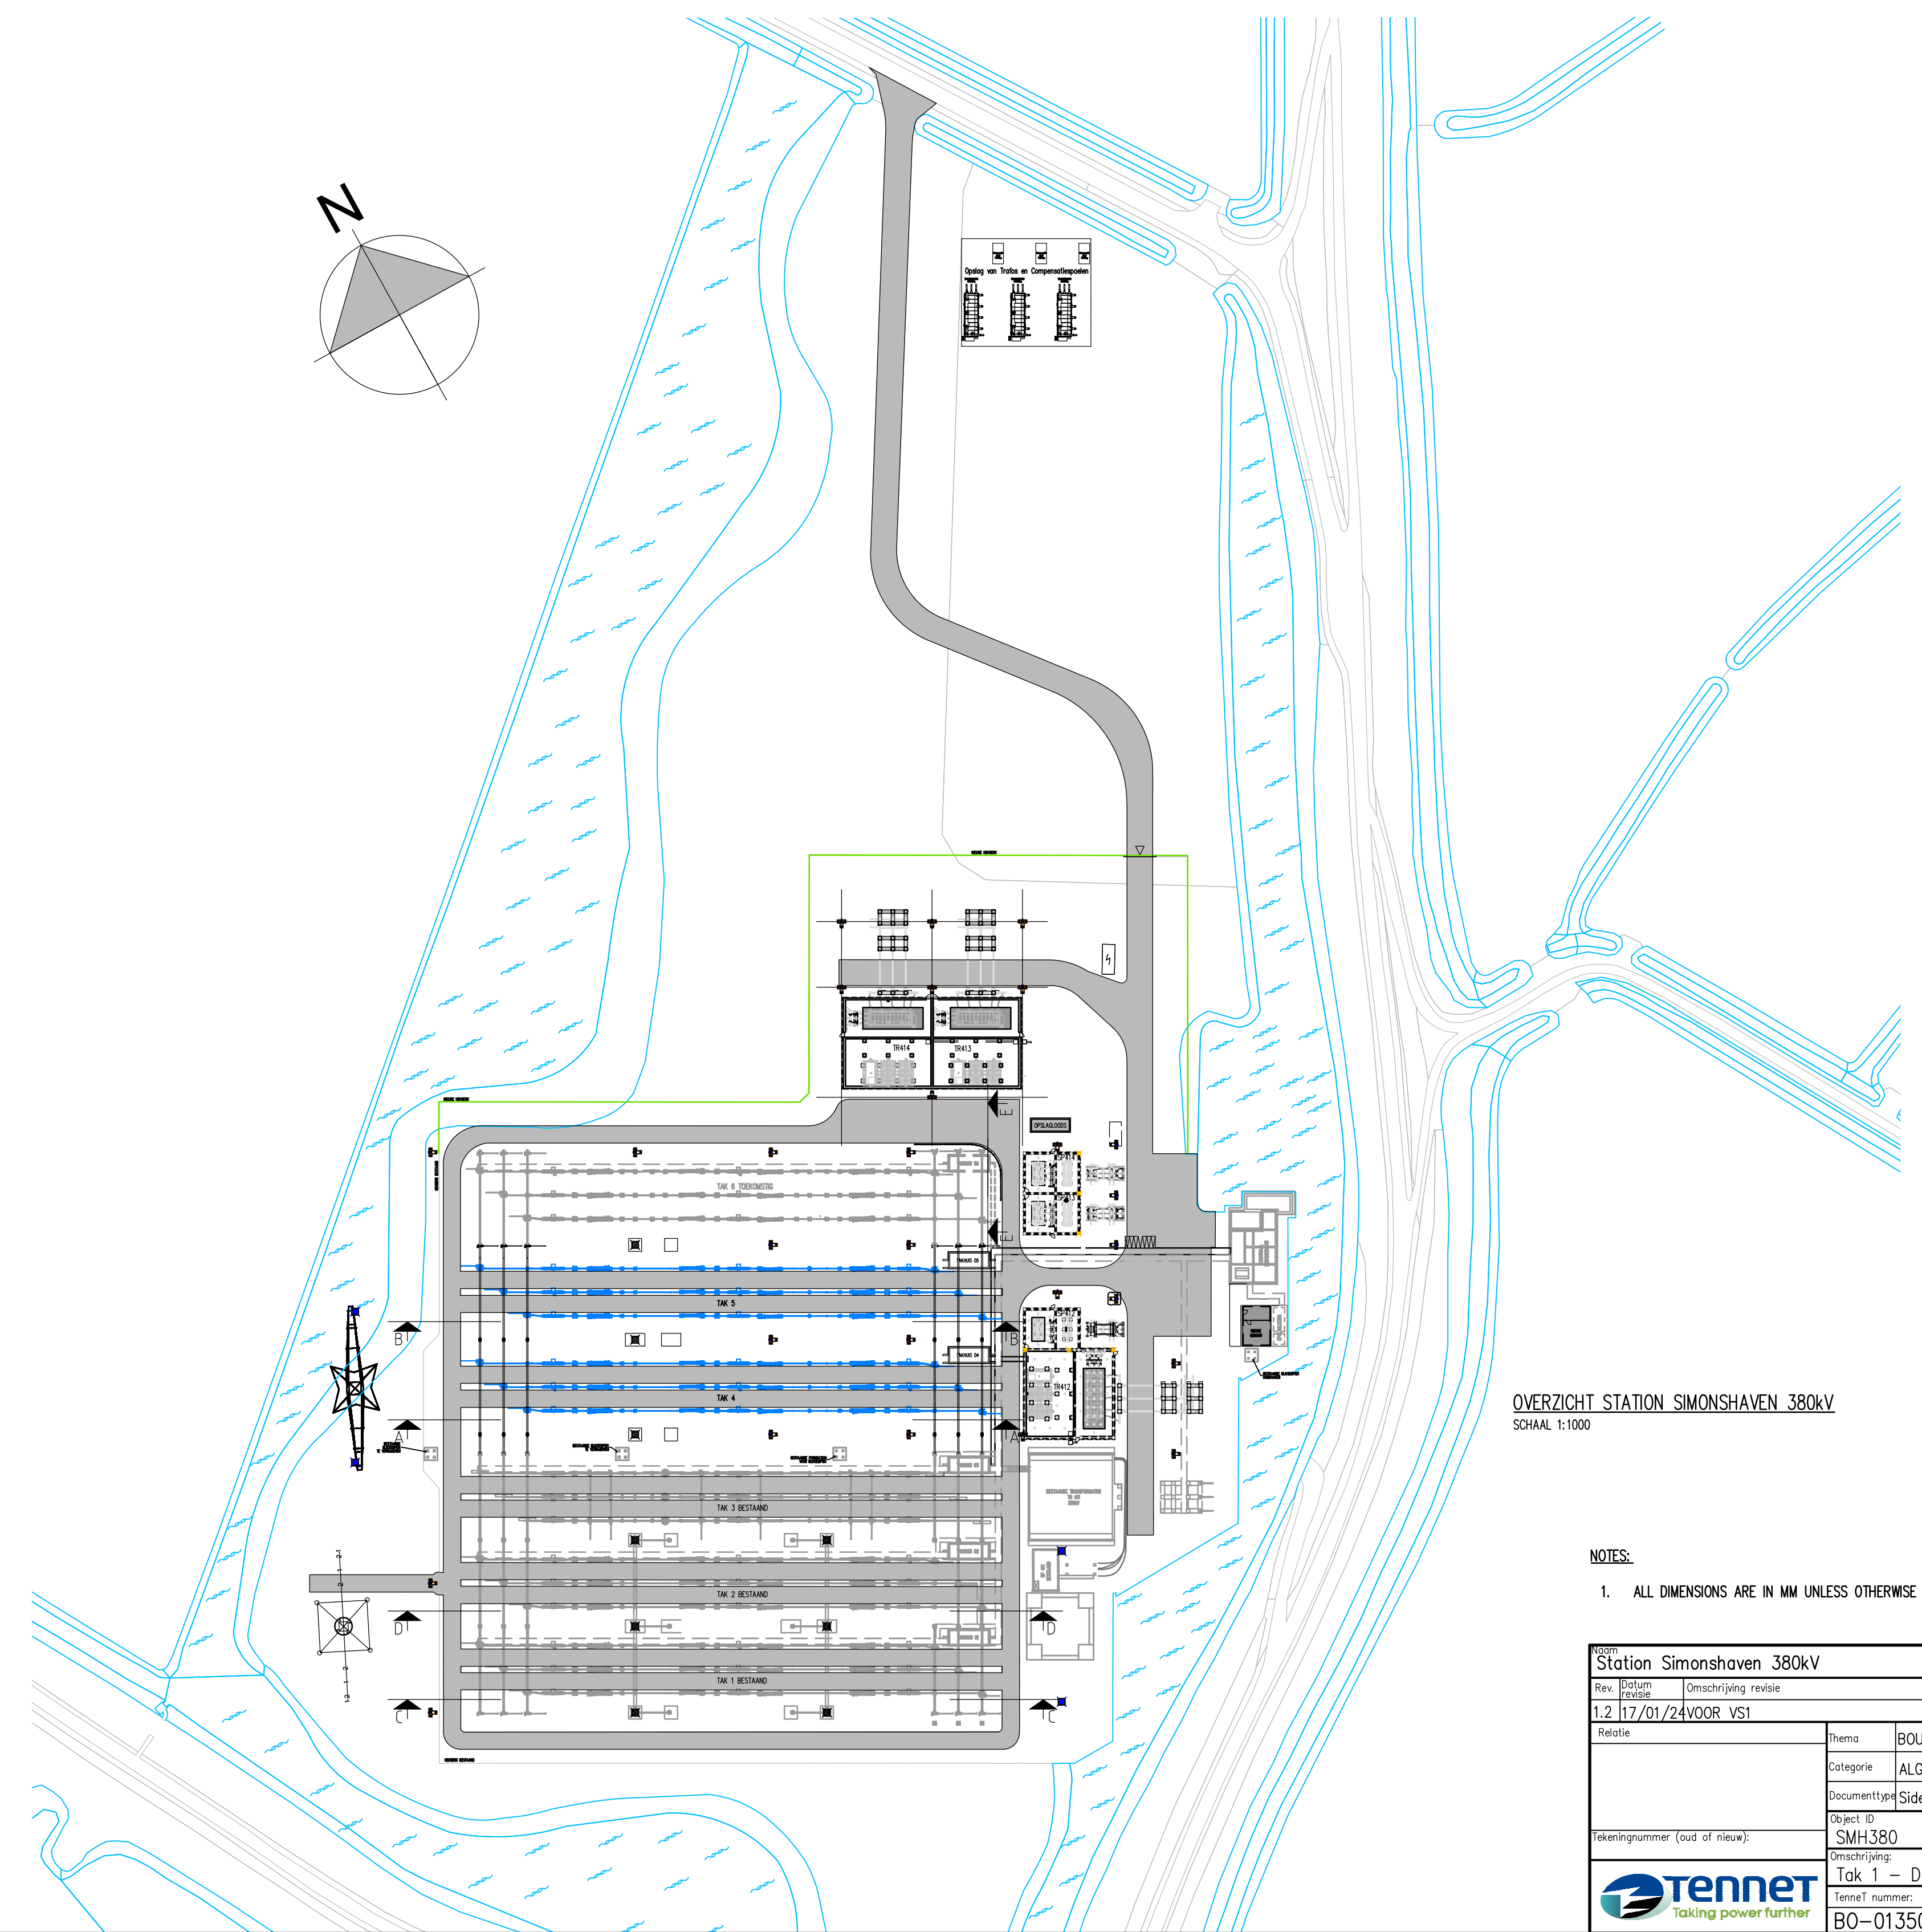


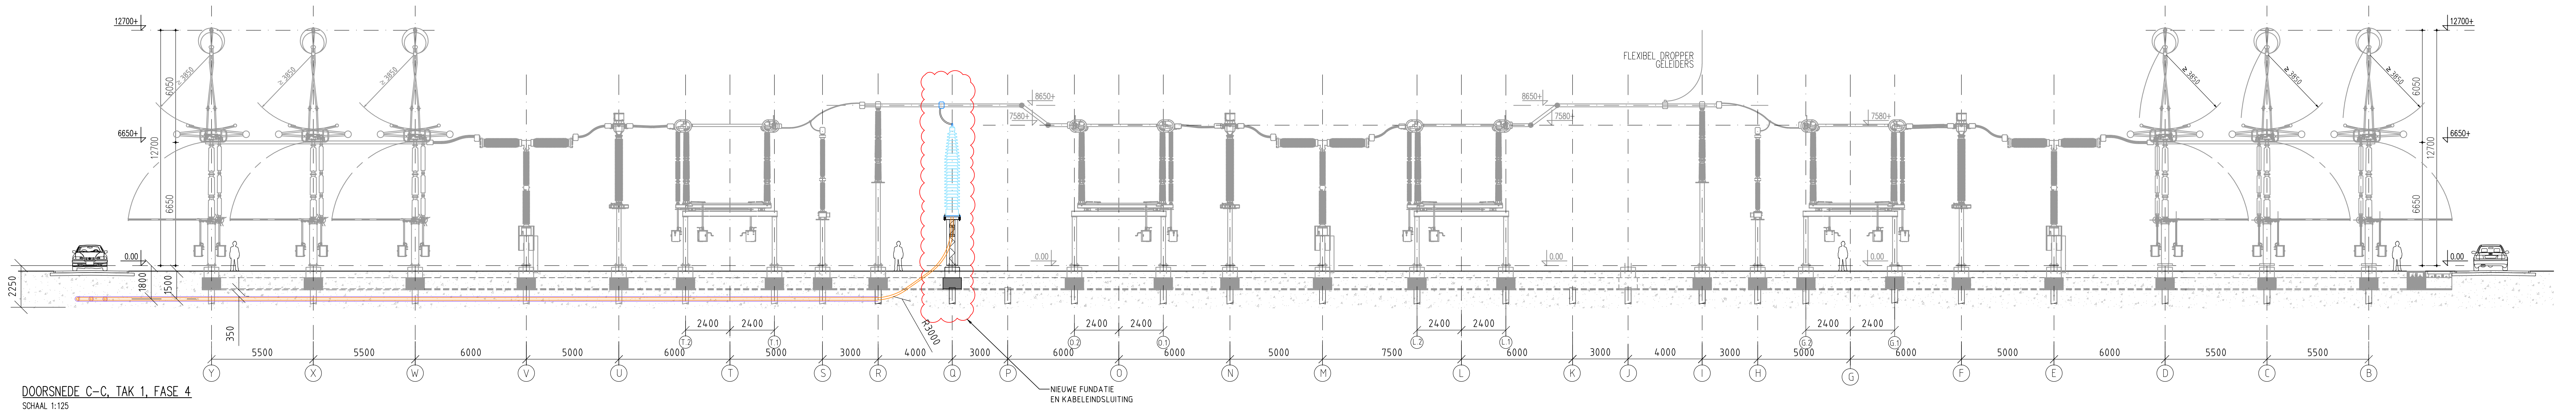

NOTES:
1. ALL DIMENSIONS ARE IN MM UNLESS OTHERWISE SPECIFIED

Project: Station Simonshaven 380kV		Revision: VOOR VS1	
Rev. 1.2	17/01/24	VOOR VS1	1.0
Revisie:		S. Behram	
Thema: BOUW EN CIVIEL		Categorie: ALGEMEEN	
Document: Side View Drawing		Object: SMH 380	
Drawing: Tak 1 - Doorsneden C-C, Phase 4		Drawing: BO-01350-04-140	
Tennet		Taking power further	