
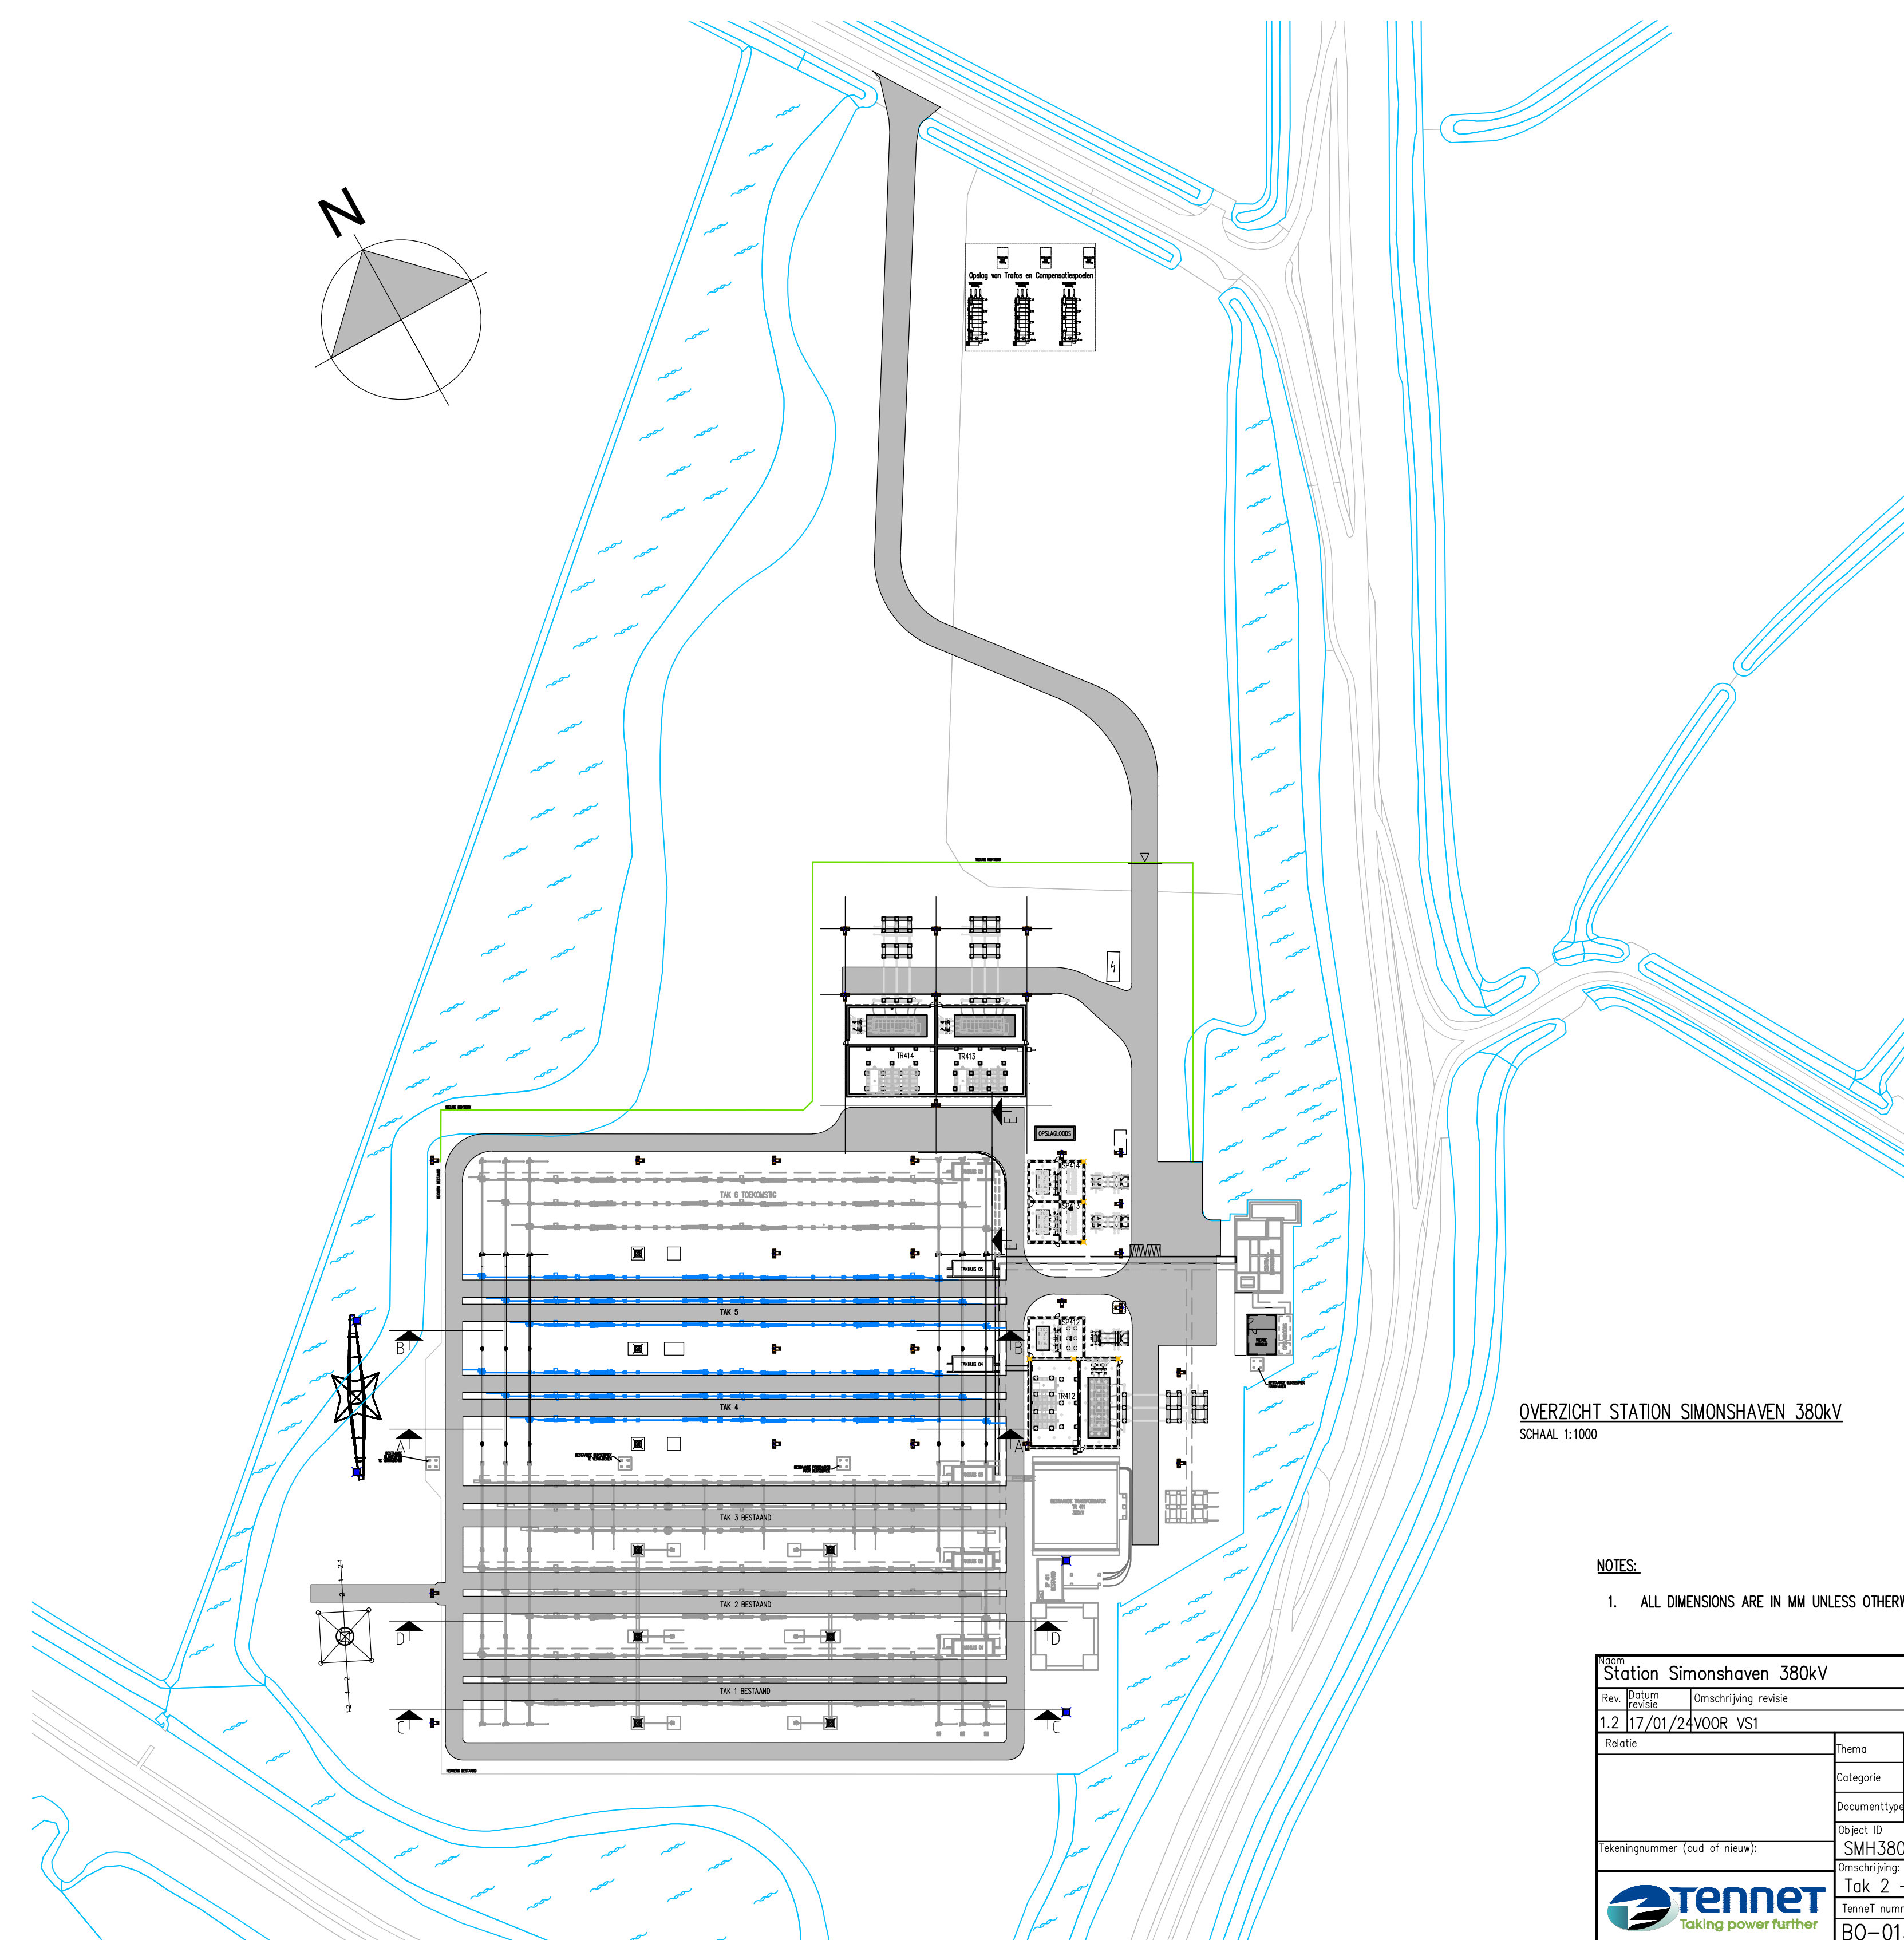


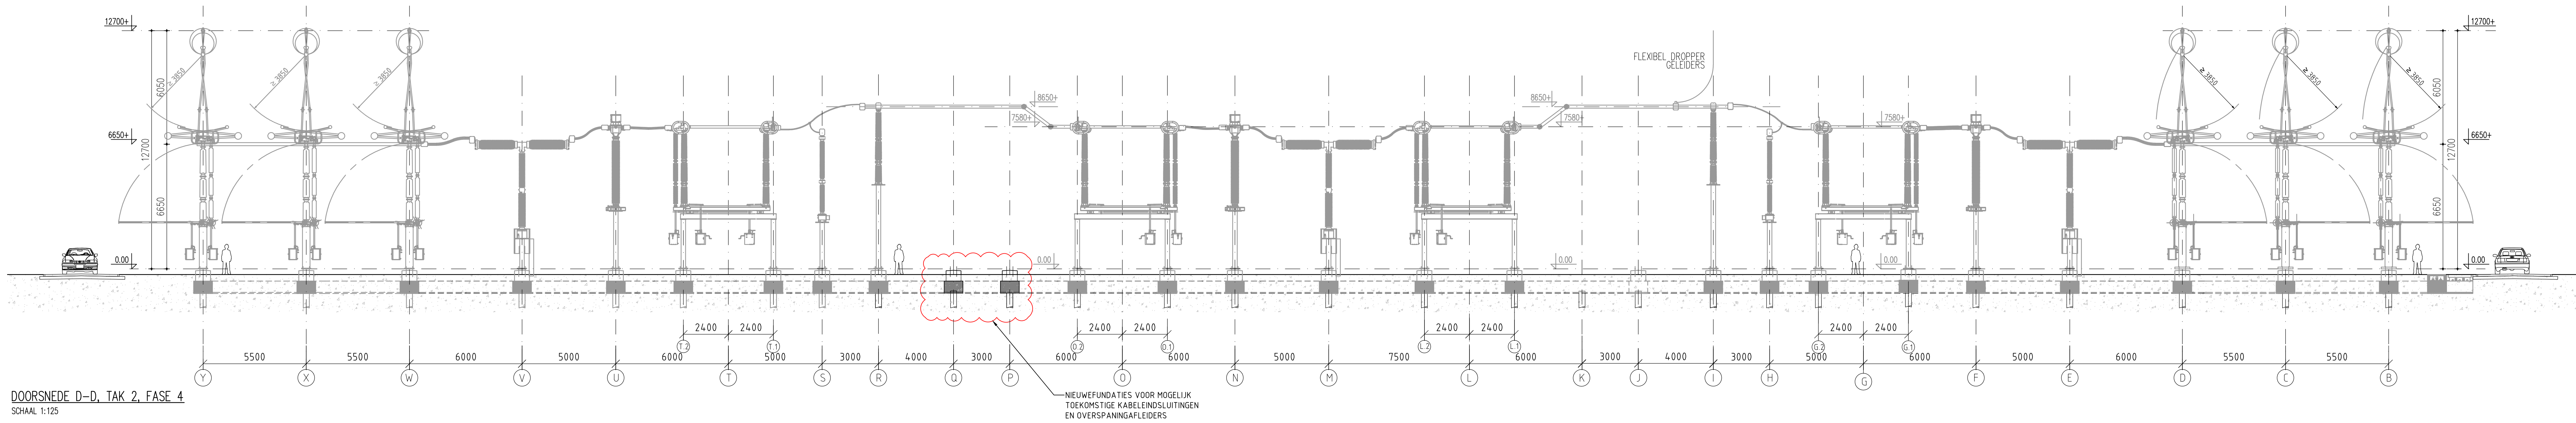

NOTES:
1. ALL DIMENSIONS ARE IN MM UNLESS OTHERWISE SPECIFIED

Project		Station Simonshaven 380kV		Revision		VOOR VS1	
Rev.	Author	Drawn	Checked	Rev.	Author	Rev.	Author
1.2	17/01/24	VOOR VS1					
Revision		Thema	PRIMAIR				
		Categorie	ALGEMEEN				
		Document type	Side View Drawing				
		Object	SMH 380				
		Project number	Tak 2 - Doorsneden D-D, Phase 4				
		Project number	BO-01350-04-141				