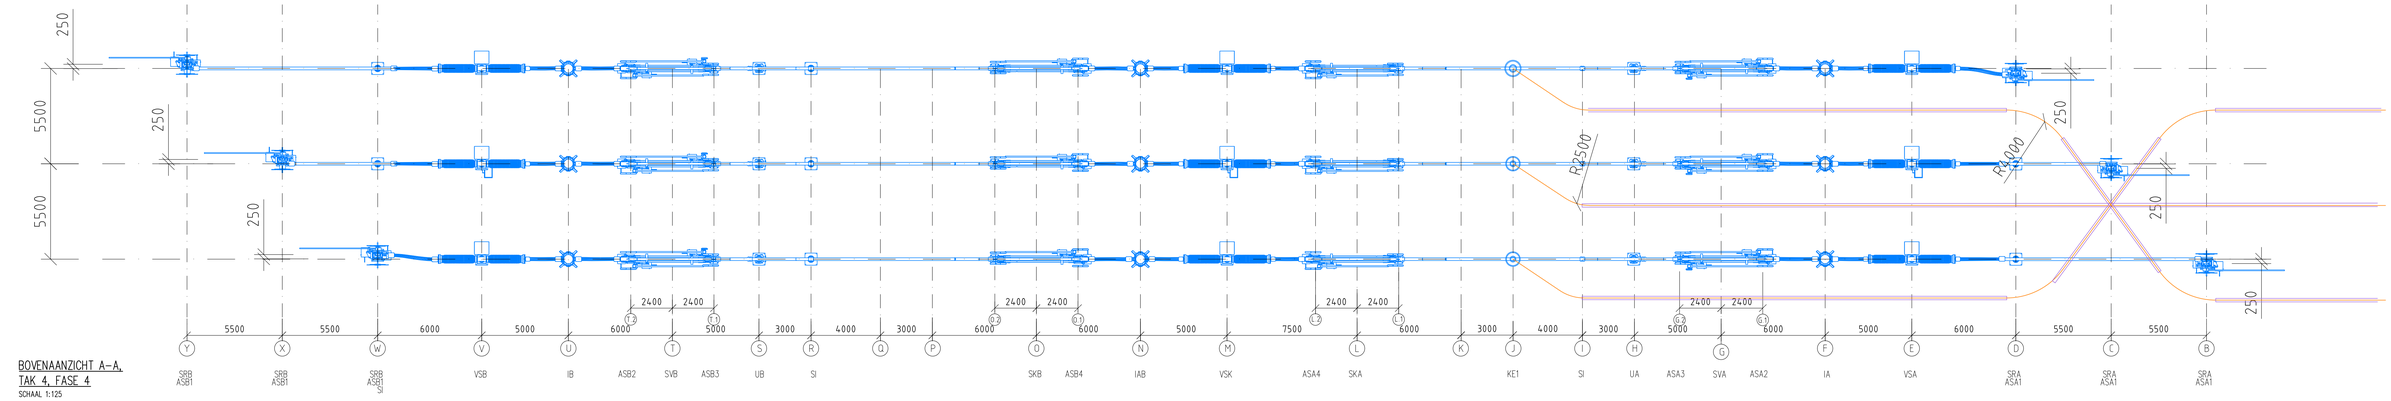

BOVENAANZICHT A–A, TAK 4, FASE 4
SCHAAL 1:125

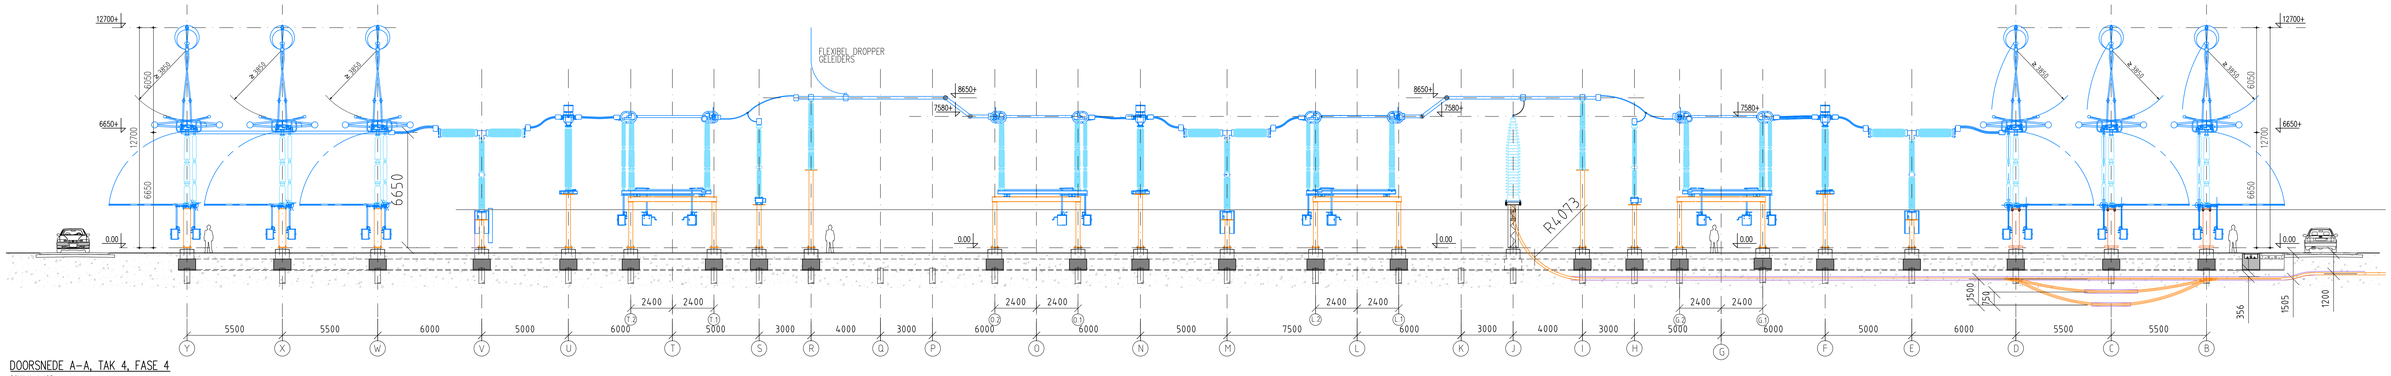

DOORSNEDE A–A, TAK 4, FASE 4
SCHAAL 1:125

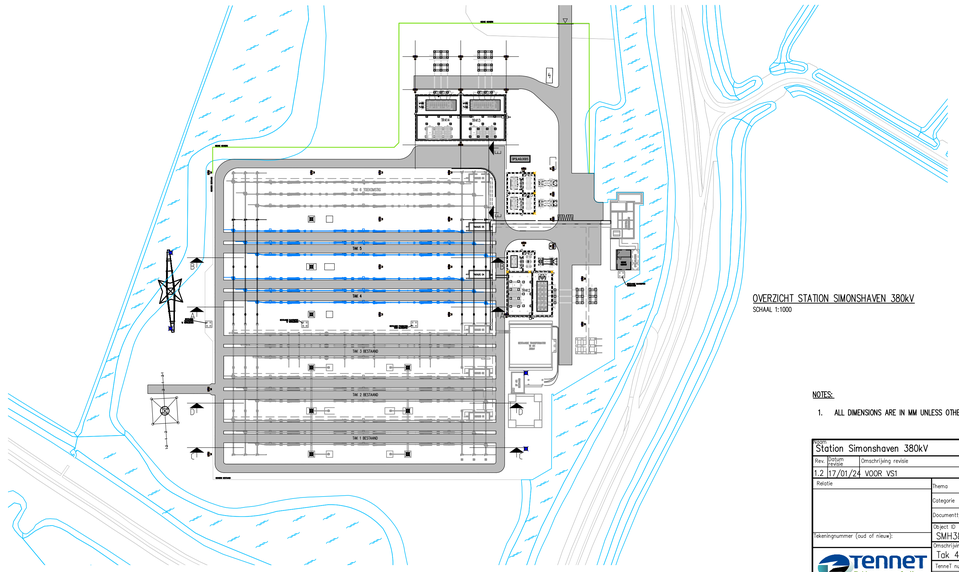

OVERZICHT STATION SIMONSHAVEN 380kV
SCHAAL 1:1000

NOTES:

1. ALL DIMENSIONS ARE IN MM UNLESS OTHERWISE SPECIFIED

Station Simonshaven 380kV				Tekeningstatus: VOOR VS1	
Rev.	Datum / Revision	Omschrijving revisie	Getekend	Datum / Ass-Bum	Schaal	Formaat
1.2	17/01/24	VOOR VS1	S.Behram/J. Gonring			A0

Relatie	Thema	PRIMAIR
	Categorie	ALGEMEEN
	Documenttype	Side View Drawing
Tekeningnummer (oud of nieuw):	Object ID	SMH380
	Omschrijving:	Tak 4 – Doorsneden A–A, Phase 4
TENNET Taking power further	TenneT nummer:	BO–01350–04–142