
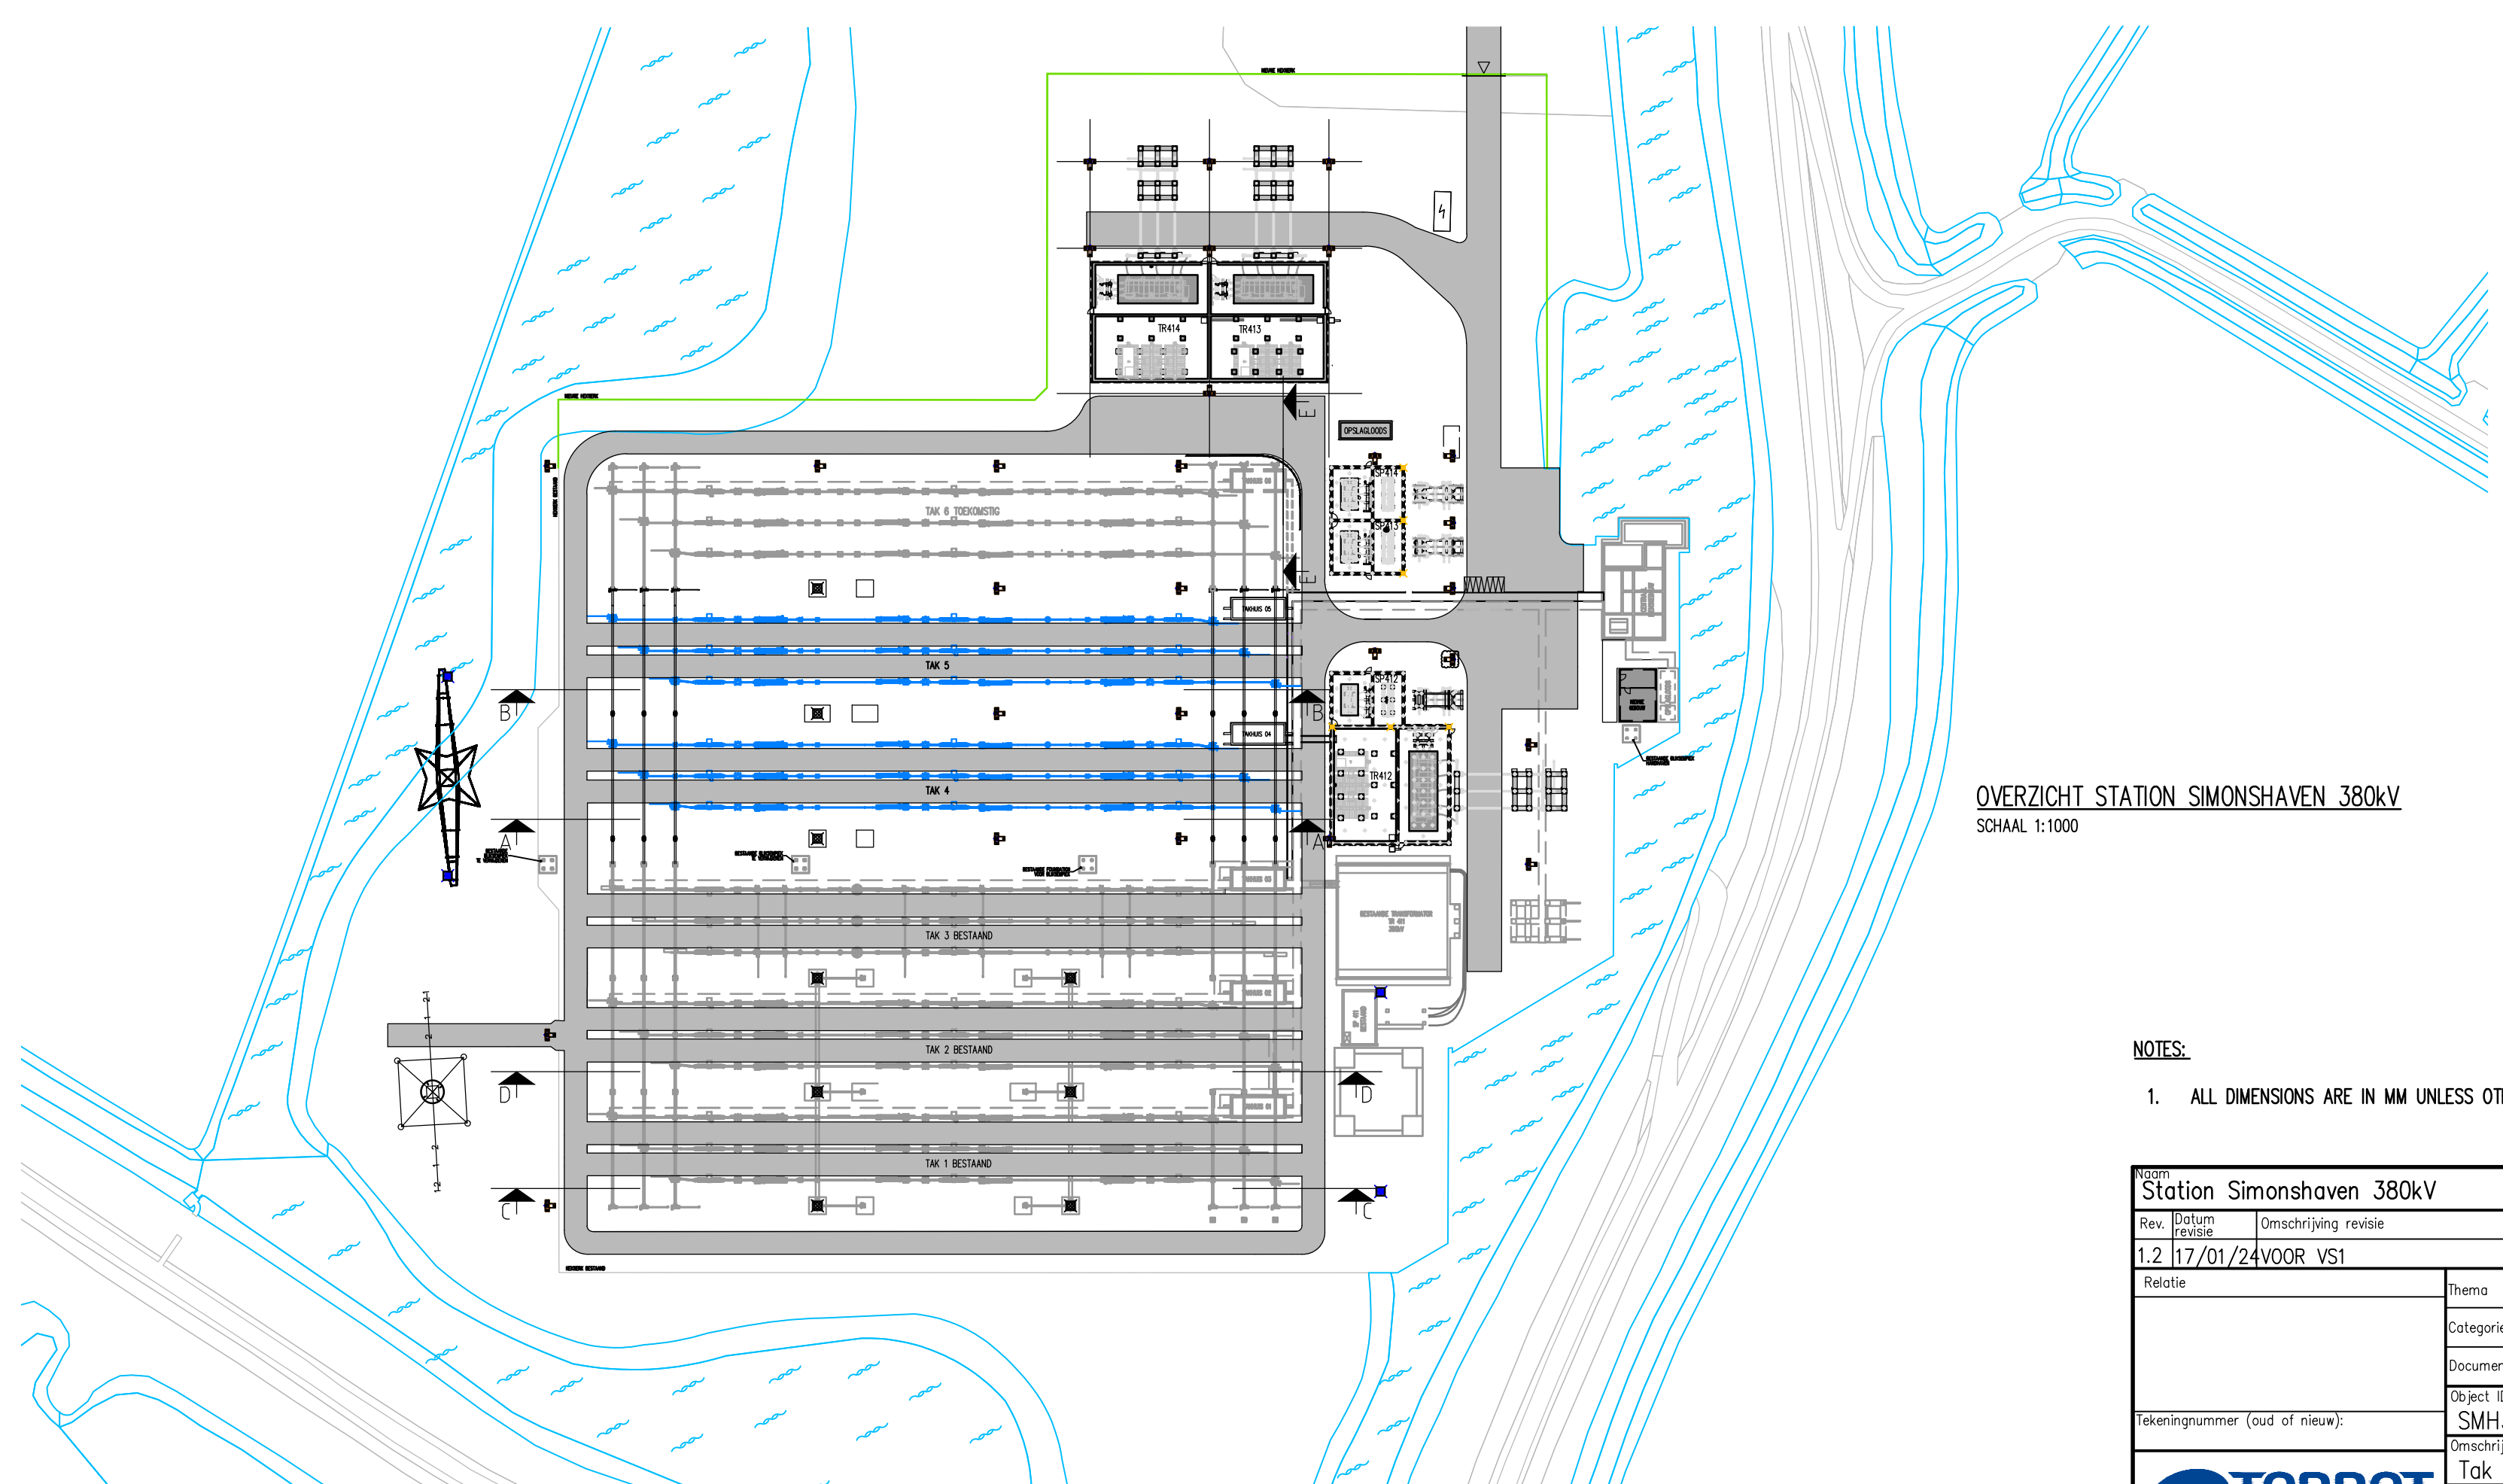


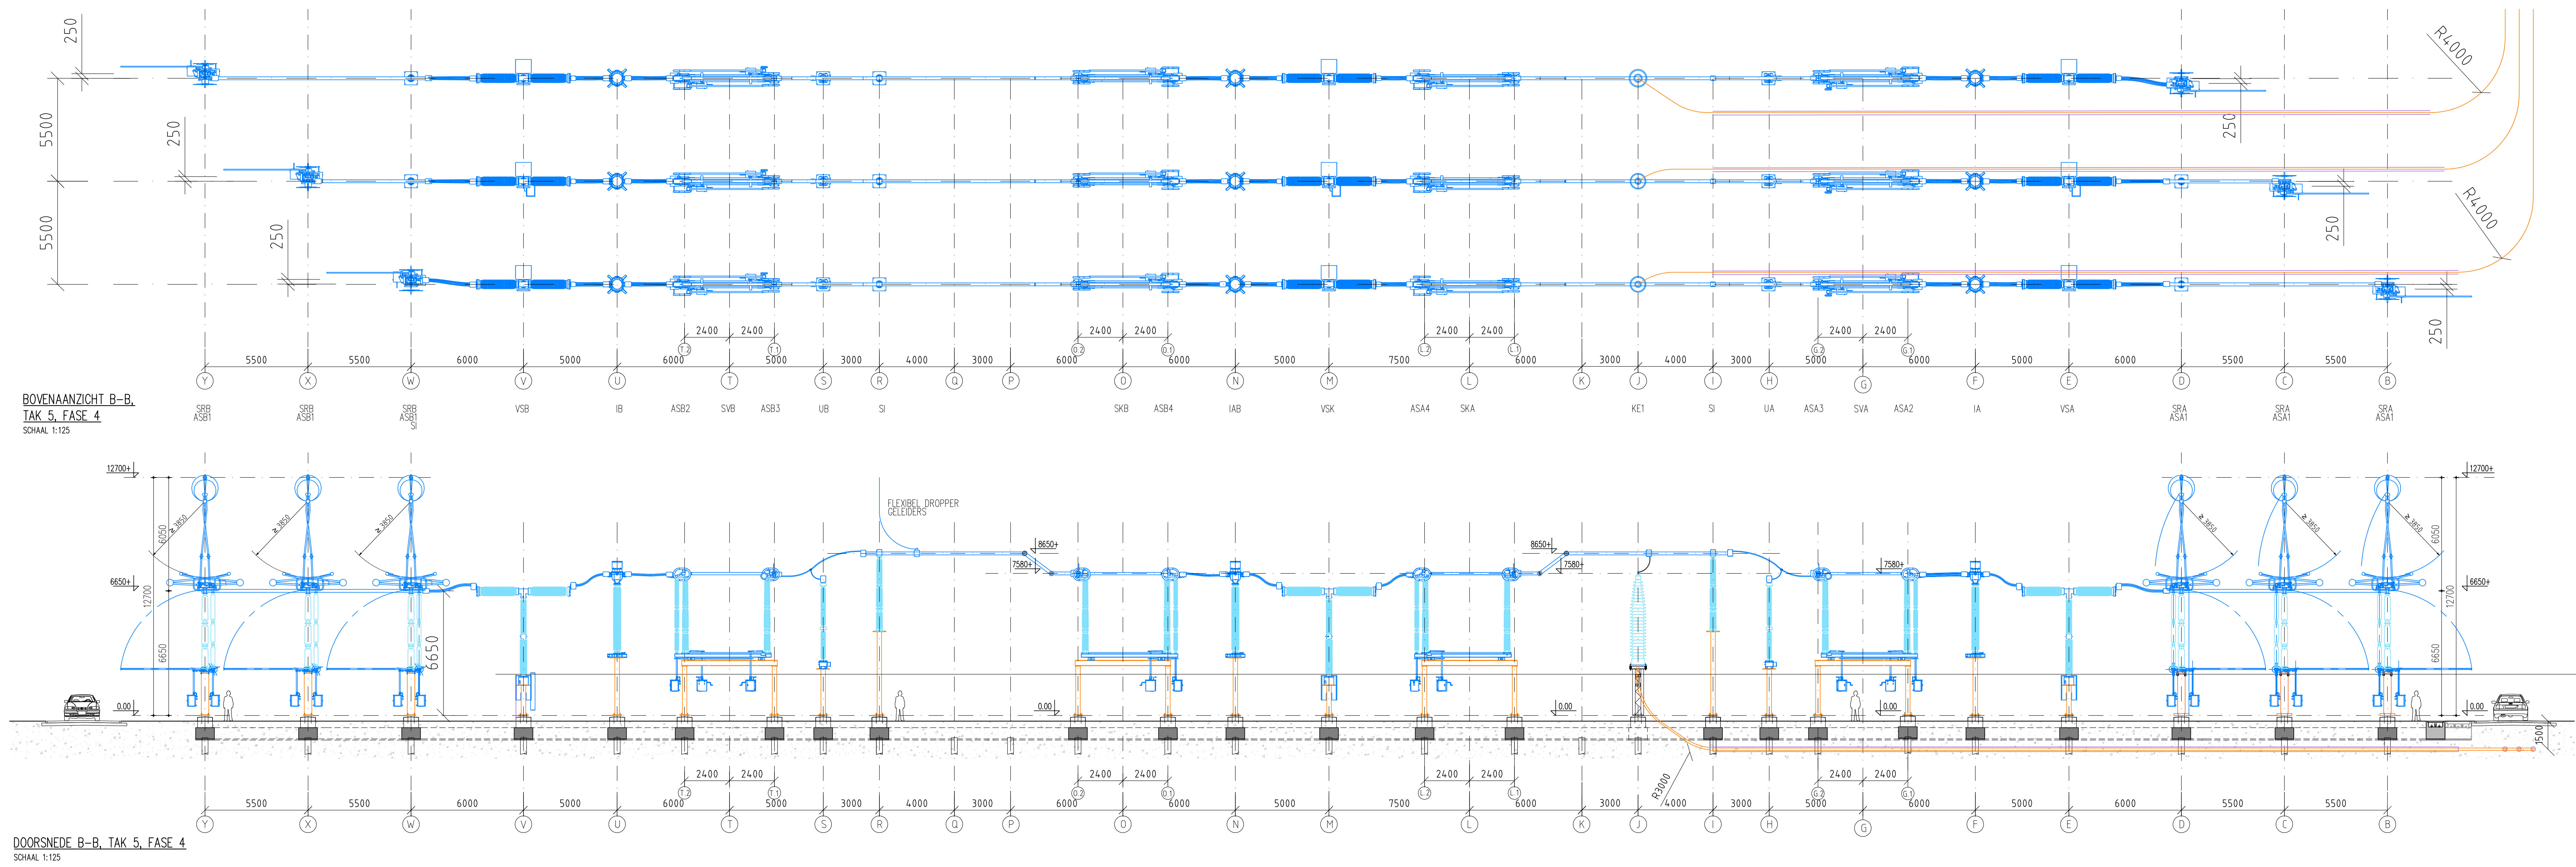

NOTES:
1. ALL DIMENSIONS ARE IN MM UNLESS OTHERWISE SPECIFIED

Project: Station Simonshaven 380kV		Revision: VOOR VS1	
Rev. 1.2	17/01/24	VOOR VS1	1.2
Author: S. Behram / J. Gonting		Scale: A0	
Theme: PRIMAIR		Category: ALGEMEEN	
Document type: Side View Drawing		Object: SMH-380	
Drawing title: Tak 5 - Doorsneden B-B, Phase 4		Drawing number: BO-01350-04-143	